
Plan armare placa cota +6.50
scara 1:50

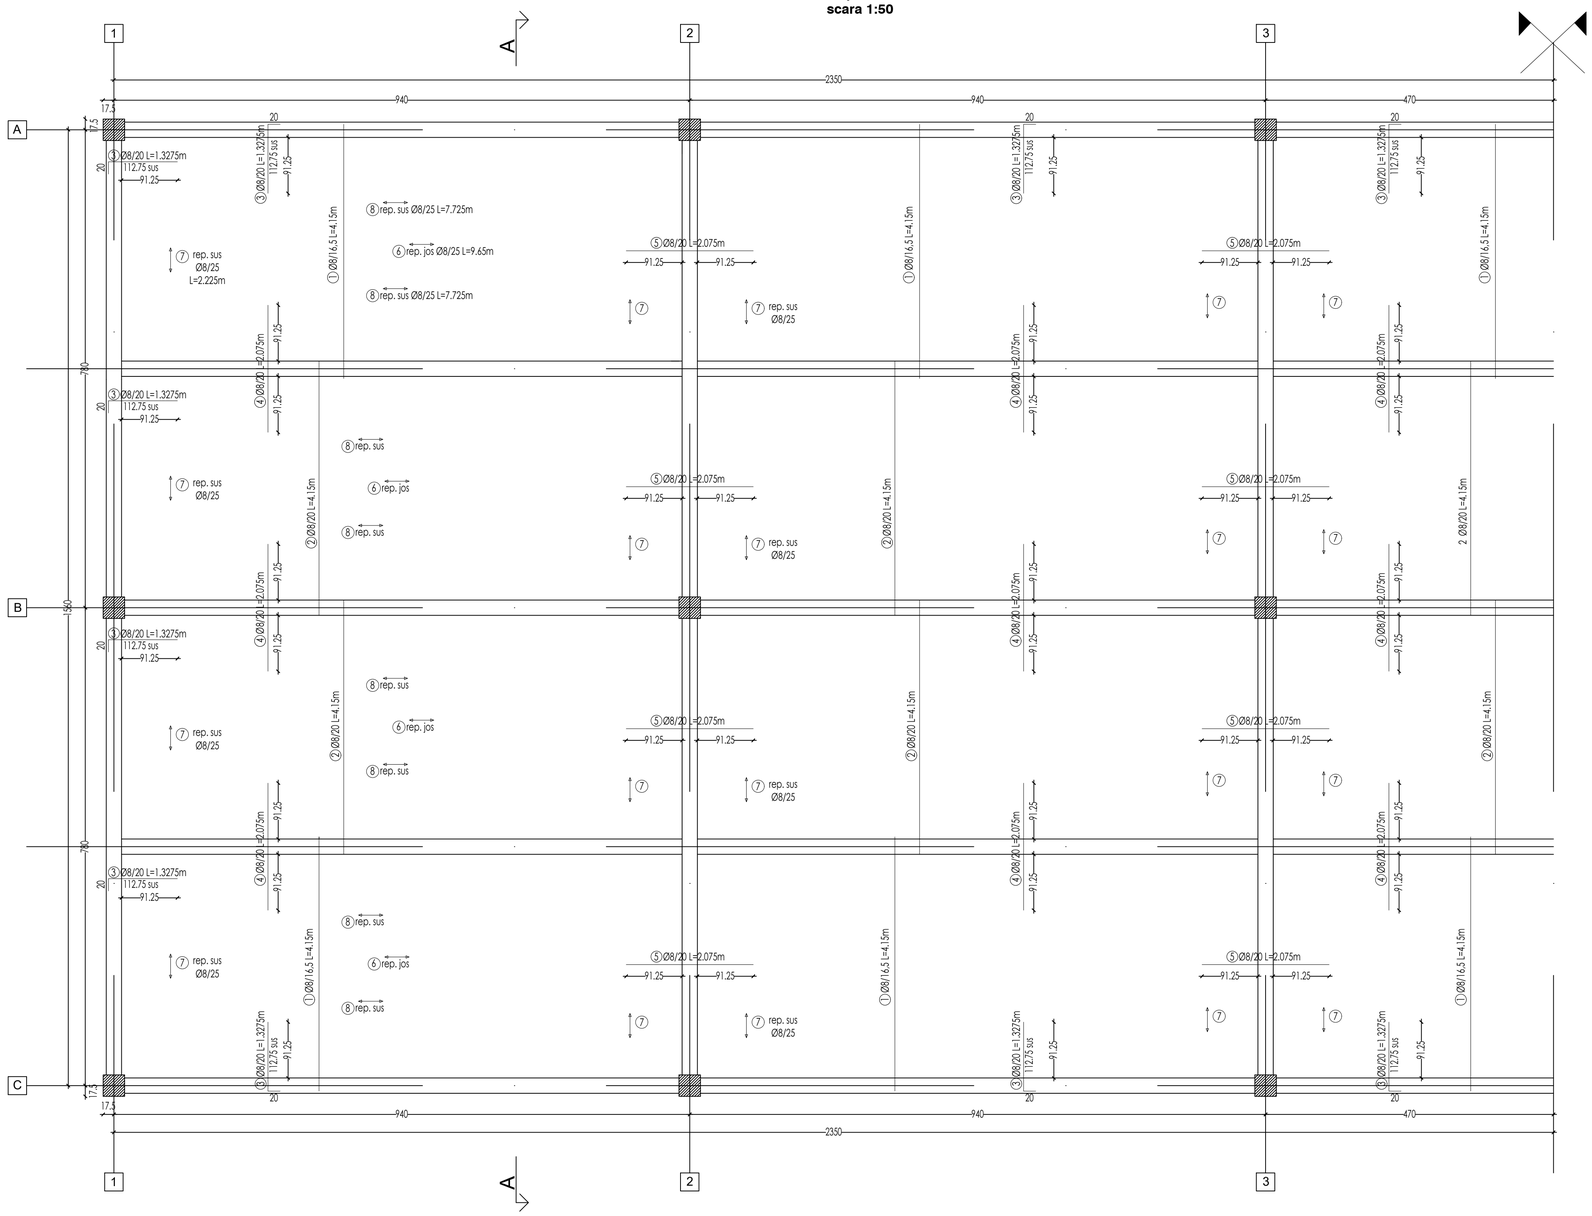

EXTRAS DE ARMĂTURI PLACĂ / OȚEL S500					
MARCA	**DIAM**	**LUNG**	**DIST. ÎNTRE BARE**	**NR. BUC.**	**LUNGIMI PE DIAMETRE**
1	8	4,15	16,5	285	1182,12
2	8	4,15	20	235	975,25
3	8	1,33	20	78	103,55
4	8	2,08	20	235	487,63
5	8	2,08	20	78	161,85
6	8	9,65	20	235	2267,75
7	8	2,23	25	188	418,30
8	8	7,73	25	188	1452,30
TOTAL LUNGIMI PE DIAMETRE [ml]					7048,74
MASA [kg/ml]					0,395
GREUTATE PE DIAMETRE [kg]					2785
GREUTATE TOTALA [kg]					**2785**


BETON CLASA:
- C25/30, XC2 - CEM II A-S 32.5R, S3, agreg. max.: 16 mm

OȚEL BETON:
-S500, cat. de ductilitate L

Acoperirea cu beton Cnom: 35 mm

UNIVERSITATEA TEHNICĂ CLUJ-NAPOCA FACULTATEA DE CONSTRUCȚII			BETON ARMAT ȘI PRECOMPRIMAT II ANUL III / SECȚIA IUDR (3631) AN UNIVERSITAR 2023-2024		PROIECT 1/2023
	NUME	SEMNĂTURĂ	SCARA 1:50	PLAN ARMARE PLACĂ cota +6.50	FAZA P.T+D.E
DESENAT	HARAPCLIC BERNARD ALEXANDRU		DATA 07.11.2023		NR. PLANȘĂ 1
VERIFICAT					

Plan cofraj placa cota +6.50
scara 1:50

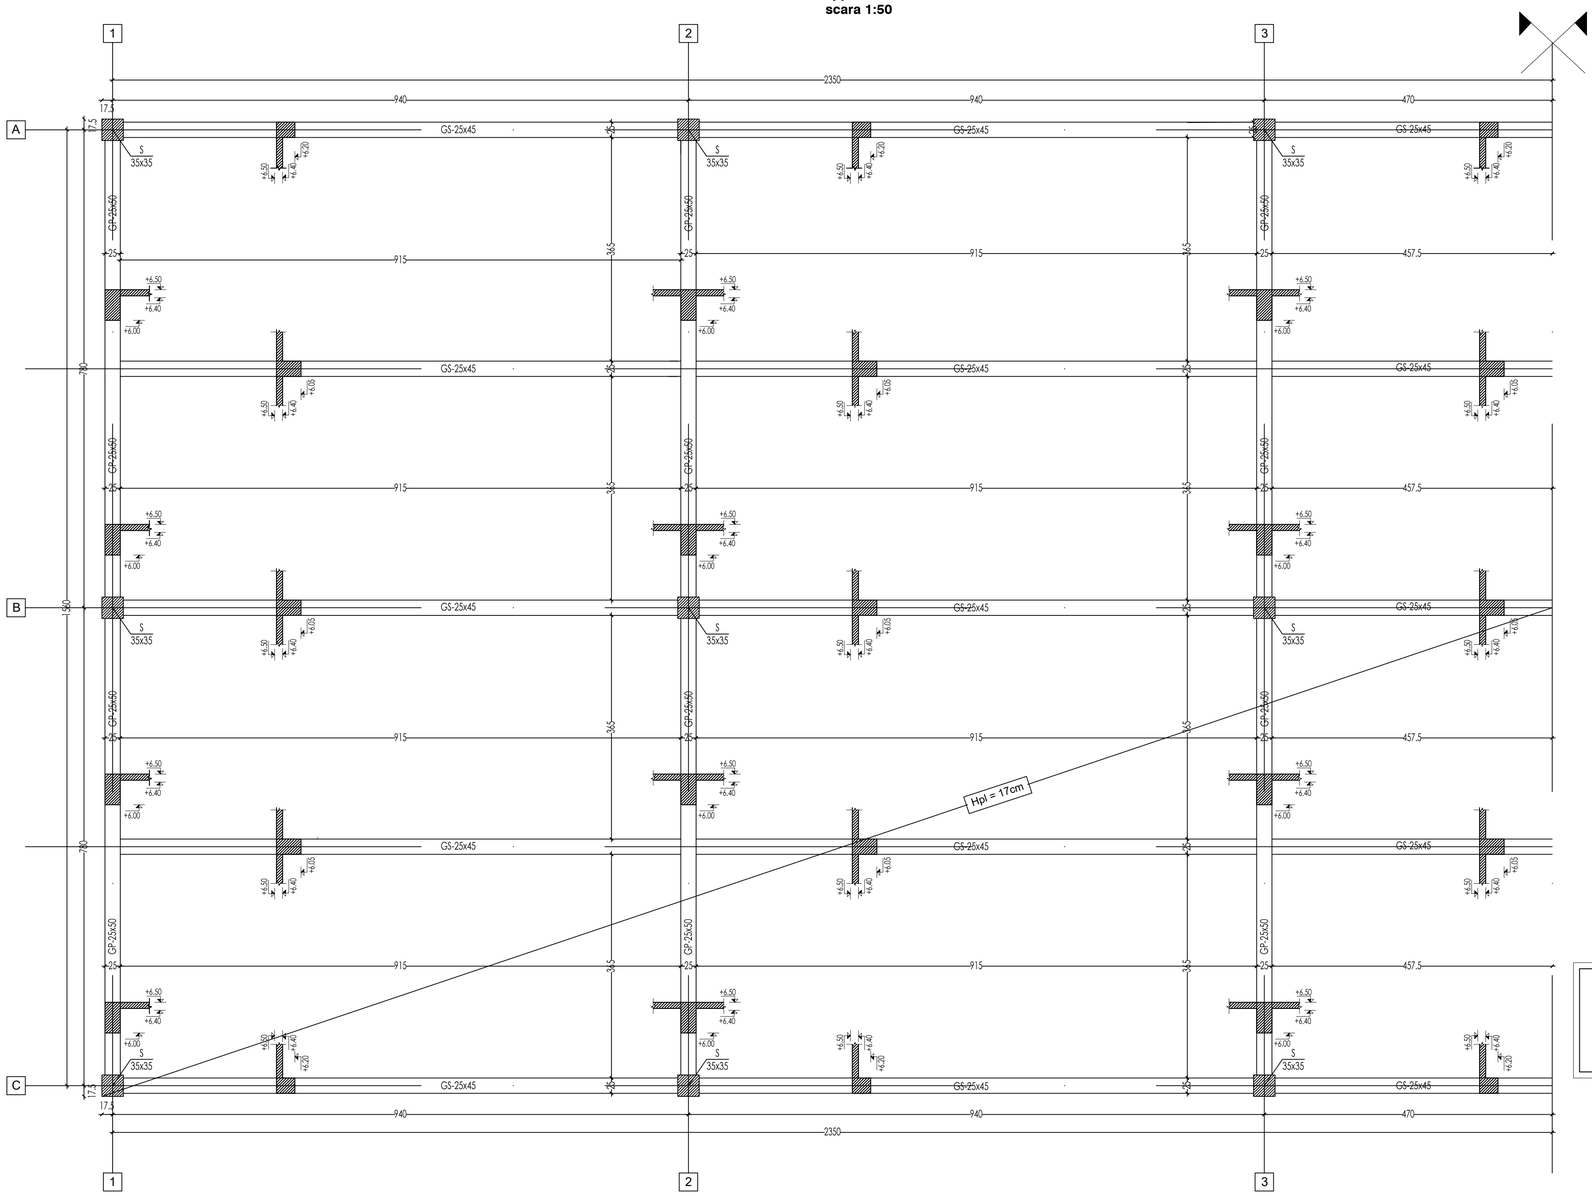


BETON CLASA:
- C25/30, XC2 - CEM II A-S 32,5R, S3, agreg. max.: 16 mm

OTEL BETON:
-S500, cat. de ductilitate L

Acoperirea cu beton Cnom: 35 mm

UNIVERSITATEA TEHNICĂ CLUJ-NAPOCA FACULTATEA DE CONSTRUCȚII			BETON ARMAT ȘI PRECOMPRIMAT II ANUL III / SECȚIA IUDR (3631) AN UNIVERSITAR 2023-2024		PROIECT 1/2023
	NUME	SEMNĂTURĂ	SCARA 1:50	PLAN COFRAJ PLACĂ cota +6.50	FAZA P.T+D.E
DESENAT	HANȚOLUC BERNARD ALEXANDRU		DATA 07.11.2023		NR. PLANȘĂ 2
VERIFICAT					

Sectiune transversala A-A
scara 1:20

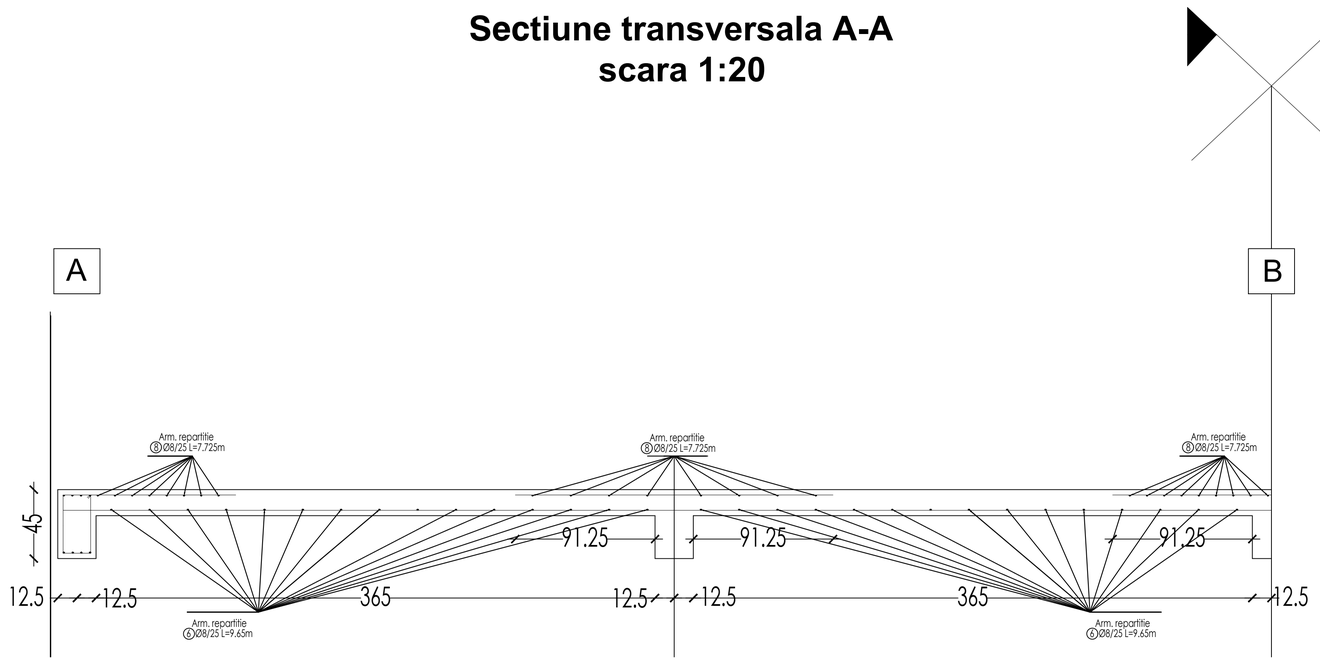


BETON CLASA:
- C25/30, XC2 - CEM II A-S 32.5R, S3,
agreg. max.: 16 mm


OȚEL BETON:
-S500, cat. de ductilitate L

Acoperirea cu beton Cnom: 35 mm


UNIVERSITATEA TEHNICĂ CLUJ-NAPOCA FACULTATEA DE CONSTRUCȚII			BETON ARMAT ȘI PRECOMPRIMAT II ANUL III / SECȚIA IUDR (3631) AN UNIVERSITAR 2023-2024		PROIECT 1/2023
	NUME	SEMNĂTURĂ	SCARA 1:20	SECȚIUNE TRANSVERSALĂ A-A	FAZA P.T+D.E
DESENAT	HARAPCIUC BERNARD ALEXANDRU		DATA 07.11.2023		NR. PLANȘĂ 3
VERIFICAT					

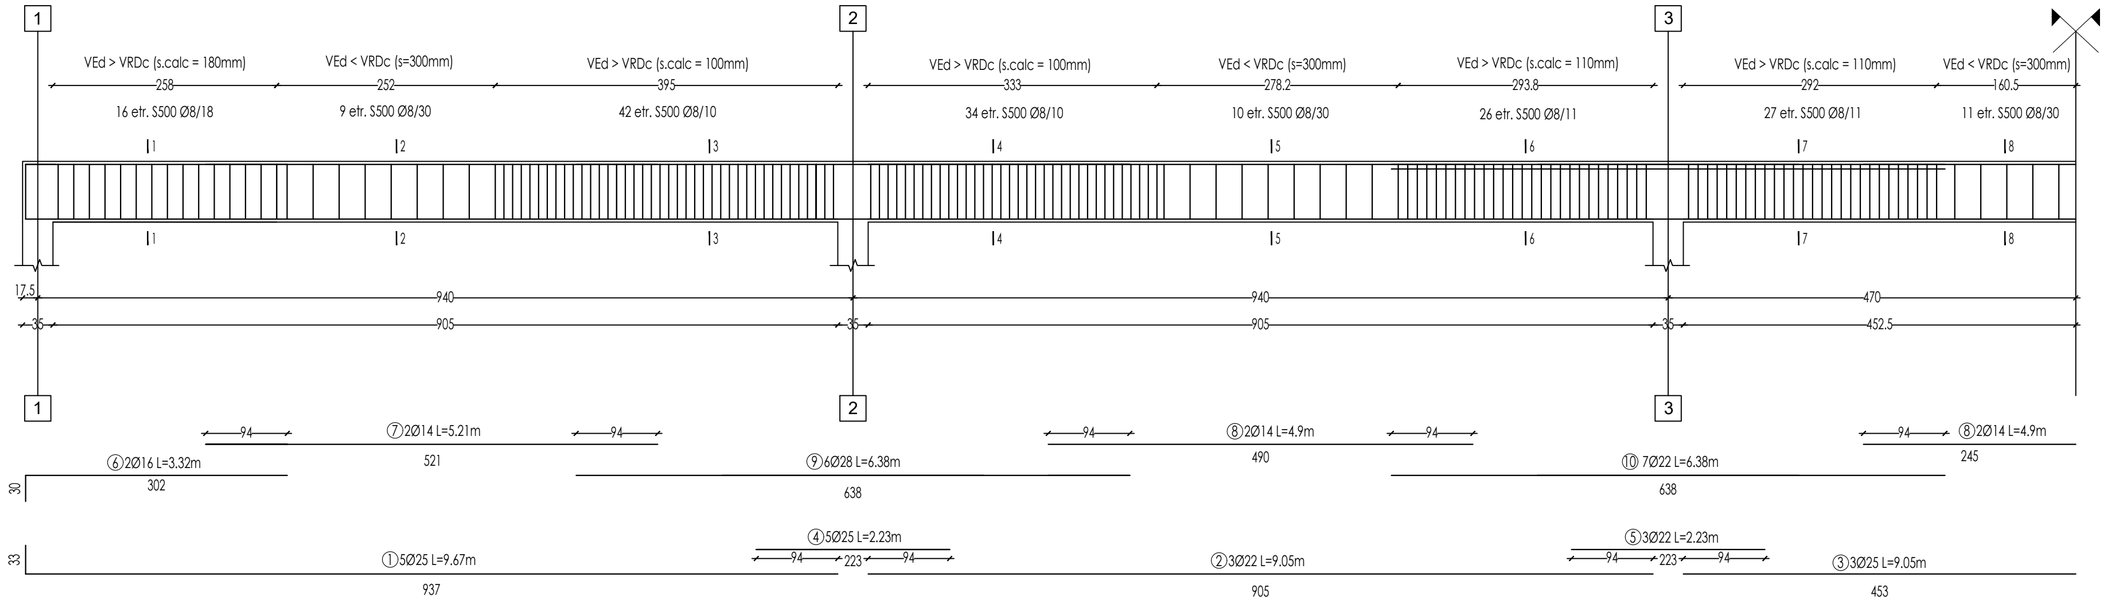


Sectiunea 1-1
scara 1:20

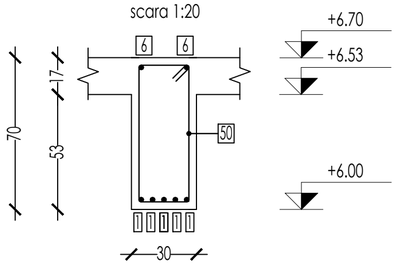


50 etr. Ø8 S500 L=1.88m

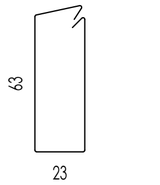


Sectiunea 2-2
scara 1:20

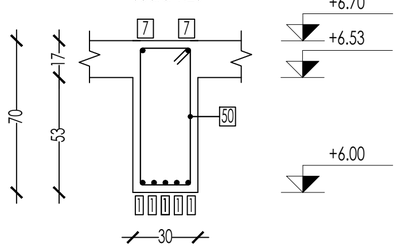


50 etr. Ø8 S500 L=1.88m

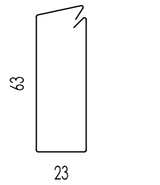


Sectiunea 3-3
scara 1:20

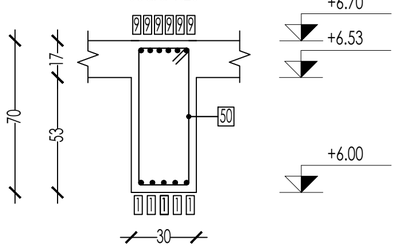


50 etr. Ø8 S500 L=1.88m

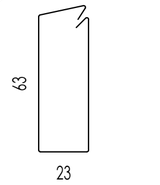


Sectiunea 4-4
scara 1:20

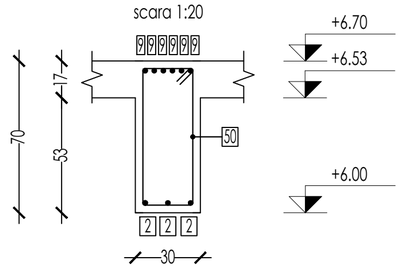


50 etr. Ø8 S500 L=1.88m

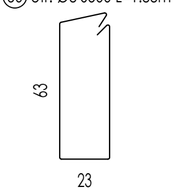


Sectiunea 5-5
scara 1:20

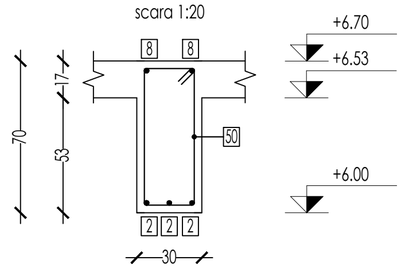


50 etr. Ø8 S500 L=1.88m

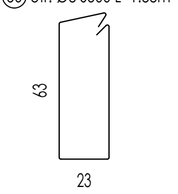


Sectiunea 6-6
scara 1:20

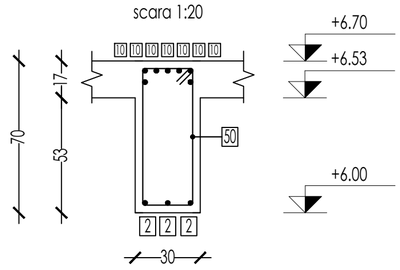


50 etr. Ø8 S500 L=1.88m

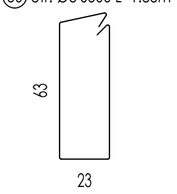


Sectiunea 7-7
scara 1:20

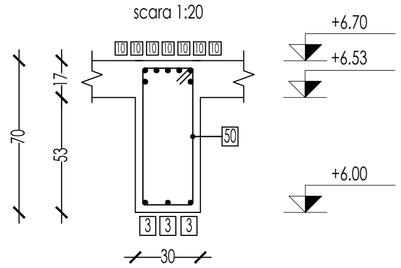


50 etr. Ø8 S500 L=1.88m

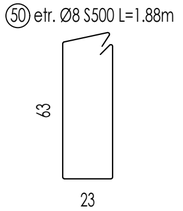

Sectiunea 8-8
scara 1:20

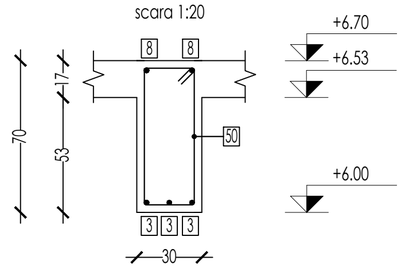

50 etr. Ø8 S500 L=1.88m

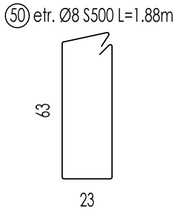

EXTRAS DE ARMĂTURI GRINZI SECUNDARE / OȚEL S500

MARCA	DIAM	LUNG	MASA [kg/ml]	NR. BUC.	LUNGIMI PE DIAMETRE [ml]	GREUTATE [kg]
50	8	1,88	0,395	1695	3186,60	1258,71
1	25	9,67	3,85	50	483,50	1861,48
2	22	9,05	2,982	30	271,50	809,61
3	25	9,05	3,85	15	135,75	522,64
4	25	2,23	3,85	50	111,50	429,28
5	22	2,23	2,982	30	66,90	199,50
6	16	3,32	1,58	20	66,40	104,91
7	14	5,21	1,21	20	104,20	126,08
8	14	4,90	1,21	30	147,00	177,87
9	28	6,38	4,835	60	382,80	1850,84
10	22	6,38	2,982	70	446,60	1331,76
TOTAL LUNGIMI PE DIAMETRE [ml]					5402,75	
GREUTATE PE DIAMETRE [kg]					8673,00	
GREUTATE TOTALA [kg]					**8673,00**	

BETON CLASA:
- C25/30, XC2 - CEM II A-S 32.5R, S3,
agreg. max.: 16 mm


OȚEL BETON:
-S500, cat. de ductilitate L

Acoperirea cu beton Cnom: 35 mm


UNIVERSITATEA TEHNICĂ CLUJ-NAPOCA FACULTATEA DE CONSTRUCȚII			BETON ARMAT ȘI PRECOMPRIMAT II ANUL III / SECȚIA IUDR (3631) AN UNIVERSITAR 2023-2024		PROIECT 1/2023
	NUME	SEMNĂTURĂ	SCARA 1:50 1:20	PLAN COFRAJ ȘI ARMARE GRINZI SECUNDARE	FAZA P.T+D.E
DESENAT	HARAPCIUC BERNARD ALEXANDRU		DATA 05.12.2023		NR. PLANȘĂ 4
VERIFICAT					

33
23
672
② 2Ø16 L=7.28m
667
③ 2Ø16 L=6.67m
7 etr. S500 Ø8/14
110
20 etr. S500 Ø8/24
468.3
hST = 600
hGP = 75
+6.75
I3
I3
35
468.3
I2
I2
I1
I1
hS = 97
±0.00
96.7
10 etr. S500 Ø8/14
127
① 2Ø16 L=1.64m
37
127
① 2Ø16 L=1.64m
37


Sectiunea 1-1
scara 1:20

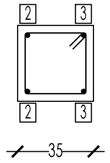


④ etr. Ø8 S500 L=1.28m

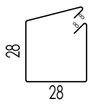


Sectiunea 2-2
scara 1:20

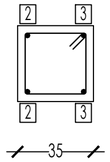


④ etr. Ø8 S500 L=1.28m

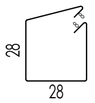

Sectiunea 3-3
scara 1:20

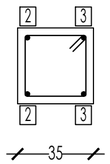

④ etr. Ø8 S500 L=1.28m

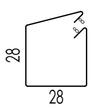

EXTRAS DE ARMĂTURI STÂLP / OȚEL S500						
MARCA	DIAM	LUNG	MASA [kg/ml]	NR. BUC.	LUNGIMI PE DIAMETRE [ml]	GREUTATE [kg]
4	8	1,28	0,395	555	710,40	280,61
3	16	6,67	1,58	30	200,10	316,16
2	16	7,28	1,58	30	218,40	345,07
1	16	1,64	1,58	60	98,40	155,47
TOTAL LUNGIMI PE DIAMETRE [ml]					1227,30	
GREUTATE PE DIAMETRE [kg]					1098,00	
GREUTATE TOTALA [kg]					**1098,00**	

BETON CLASA:
- C25/30, XC2 - CEM II A-S 32.5R, S3, agreg. max.: 16 mm

OTEL BETON:
-S500, cat. de ductilitate L

Acoperirea cu beton Cnom: 35 mm

UNIVERSITATEA TEHNICĂ CLUJ-NAPOCA FACULTATEA DE CONSTRUCȚII			BETON ARMAT ȘI PRECOMPRIMAT II ANUL III / SECȚIA IUDR (3631) AN UNIVERSITAR 2023-2024		PROIECT 1/2023
	NUME	SEMNĂTURĂ	SCARA 1:20	PLAN COFRAJ ȘI ARMARE STÂLP	FAZA P.T+D.E
DESENAT	HARAPCIUC BERNARD ALEXANDRU		DATA 16.01.2024		NR. PLANȘĂ 5
VERIFICAT					