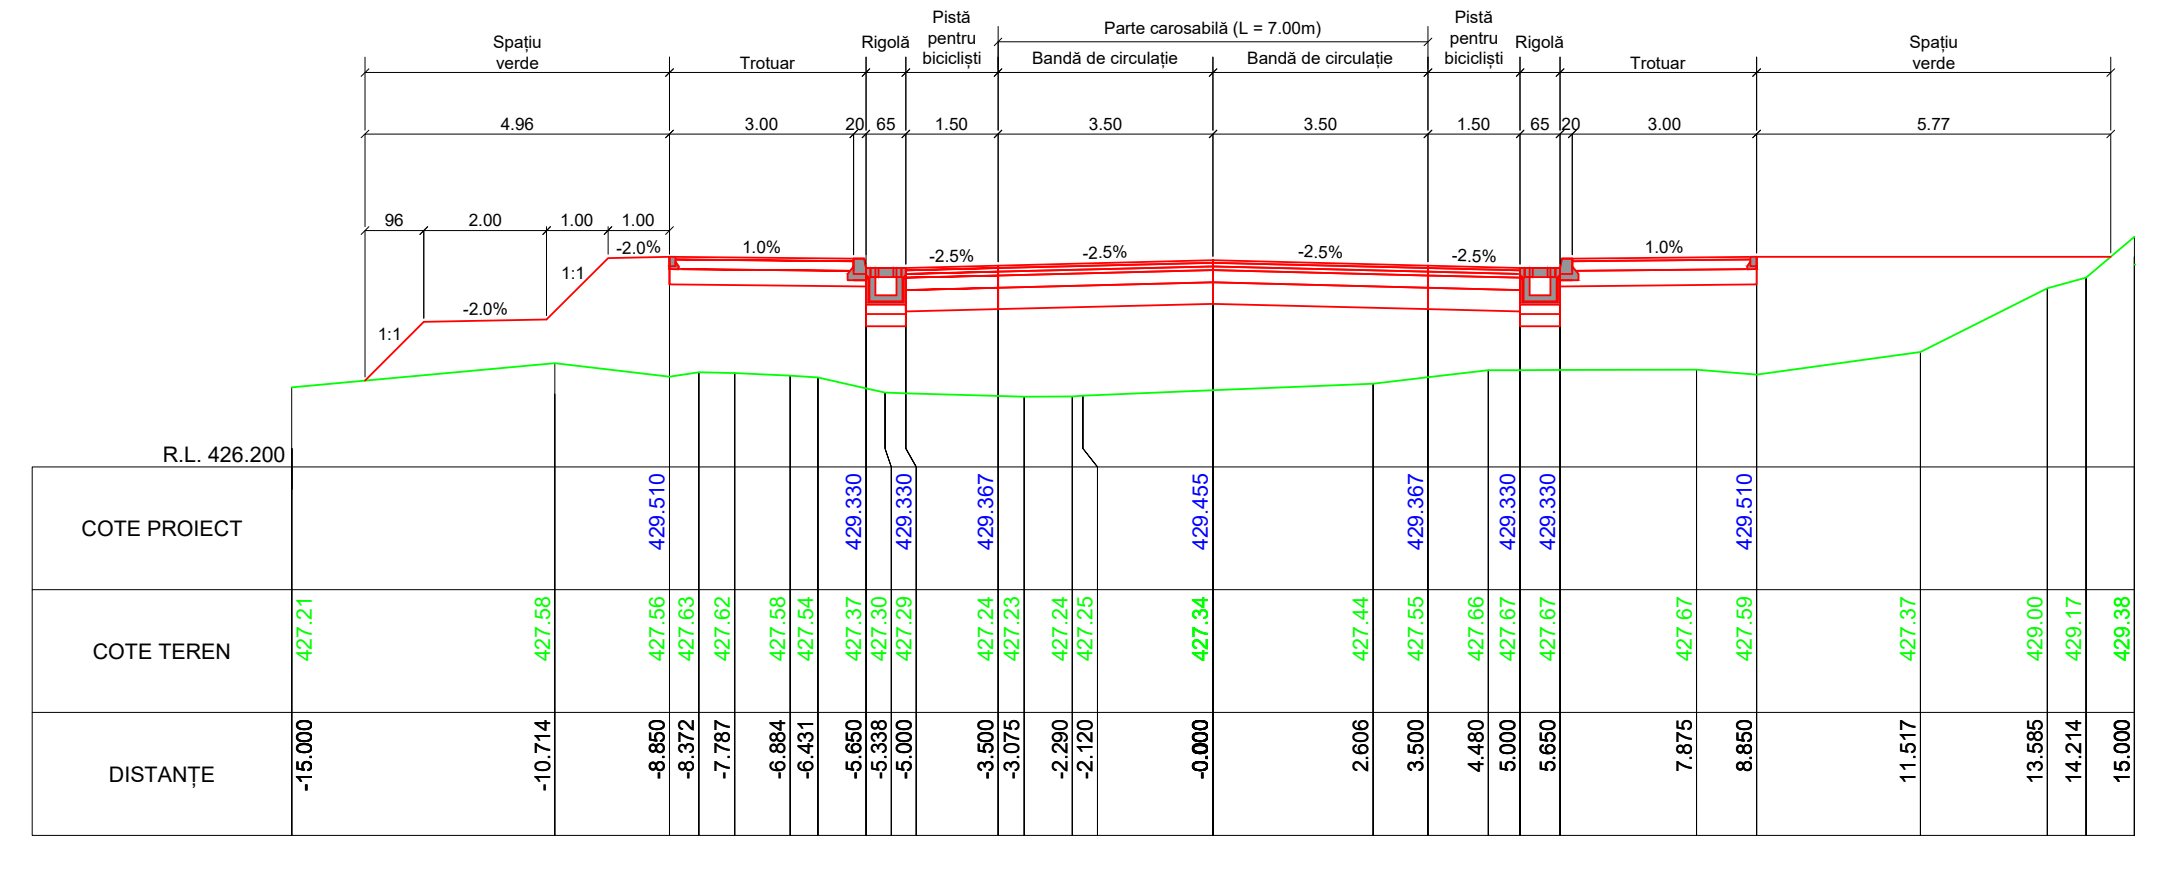
Km 0.000 (început traseu)

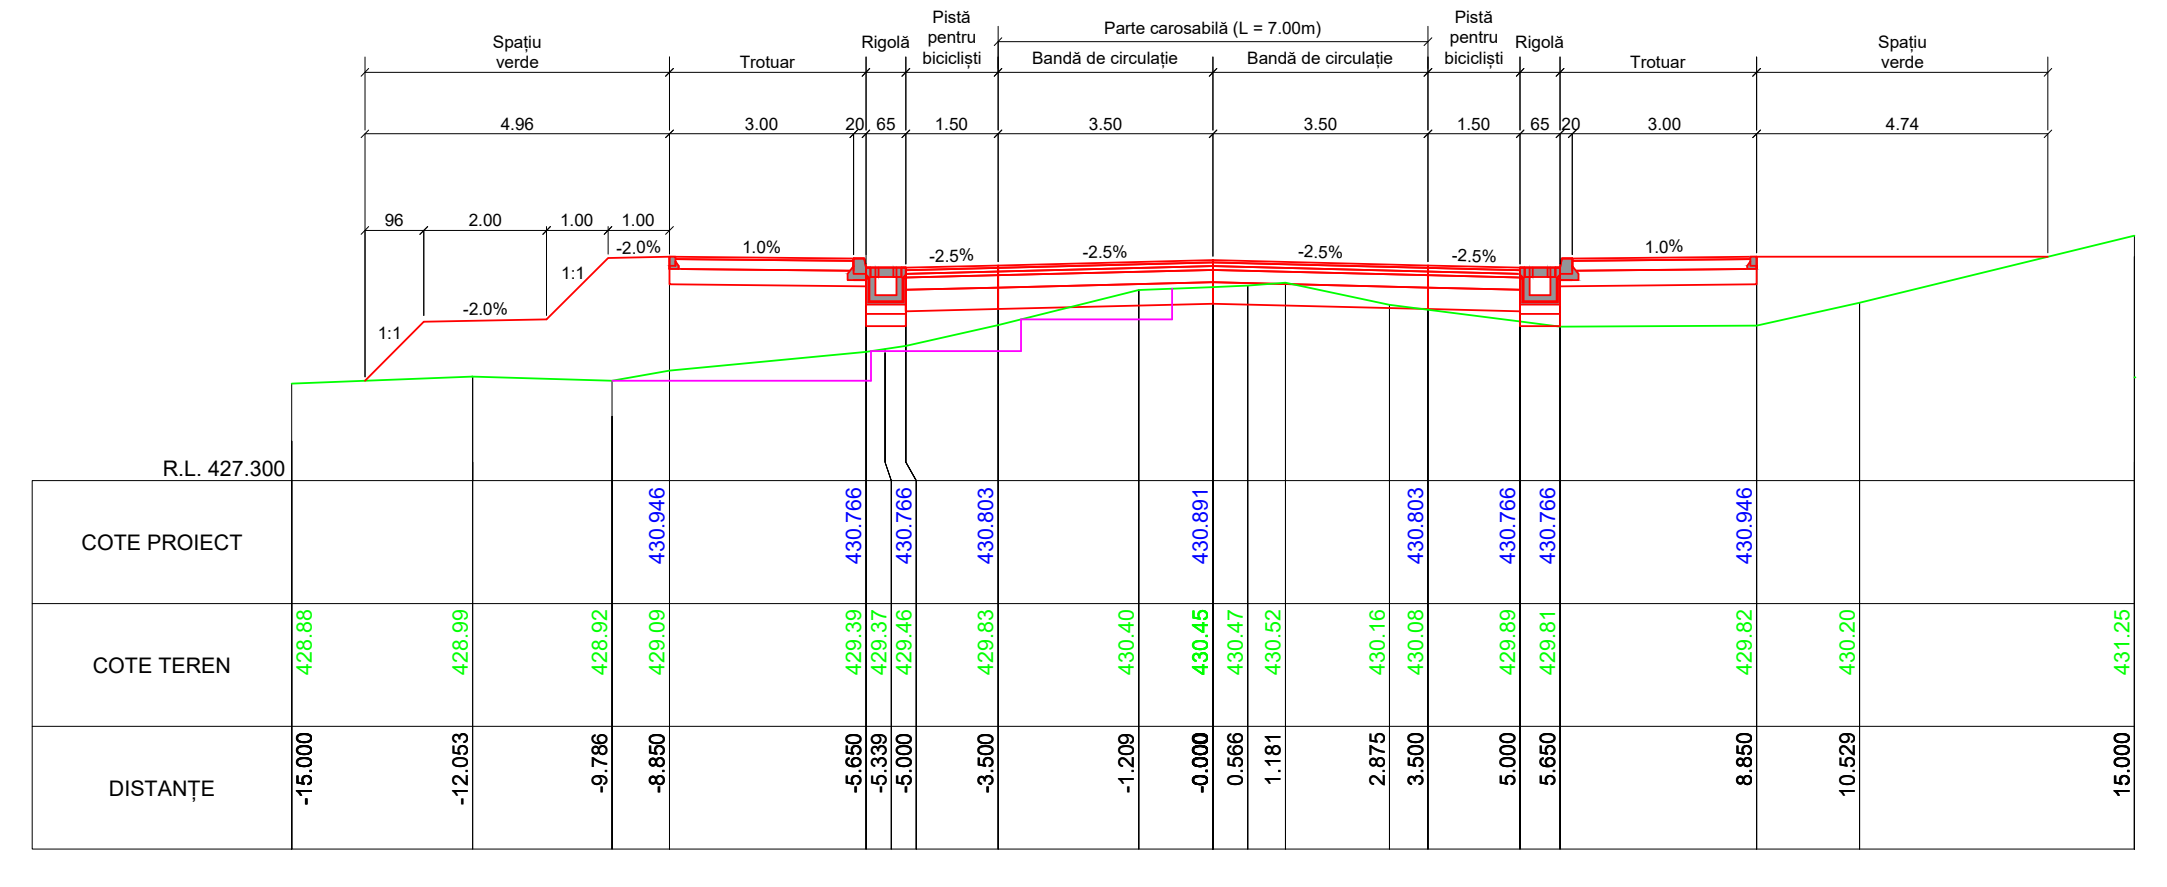
Km 30.000

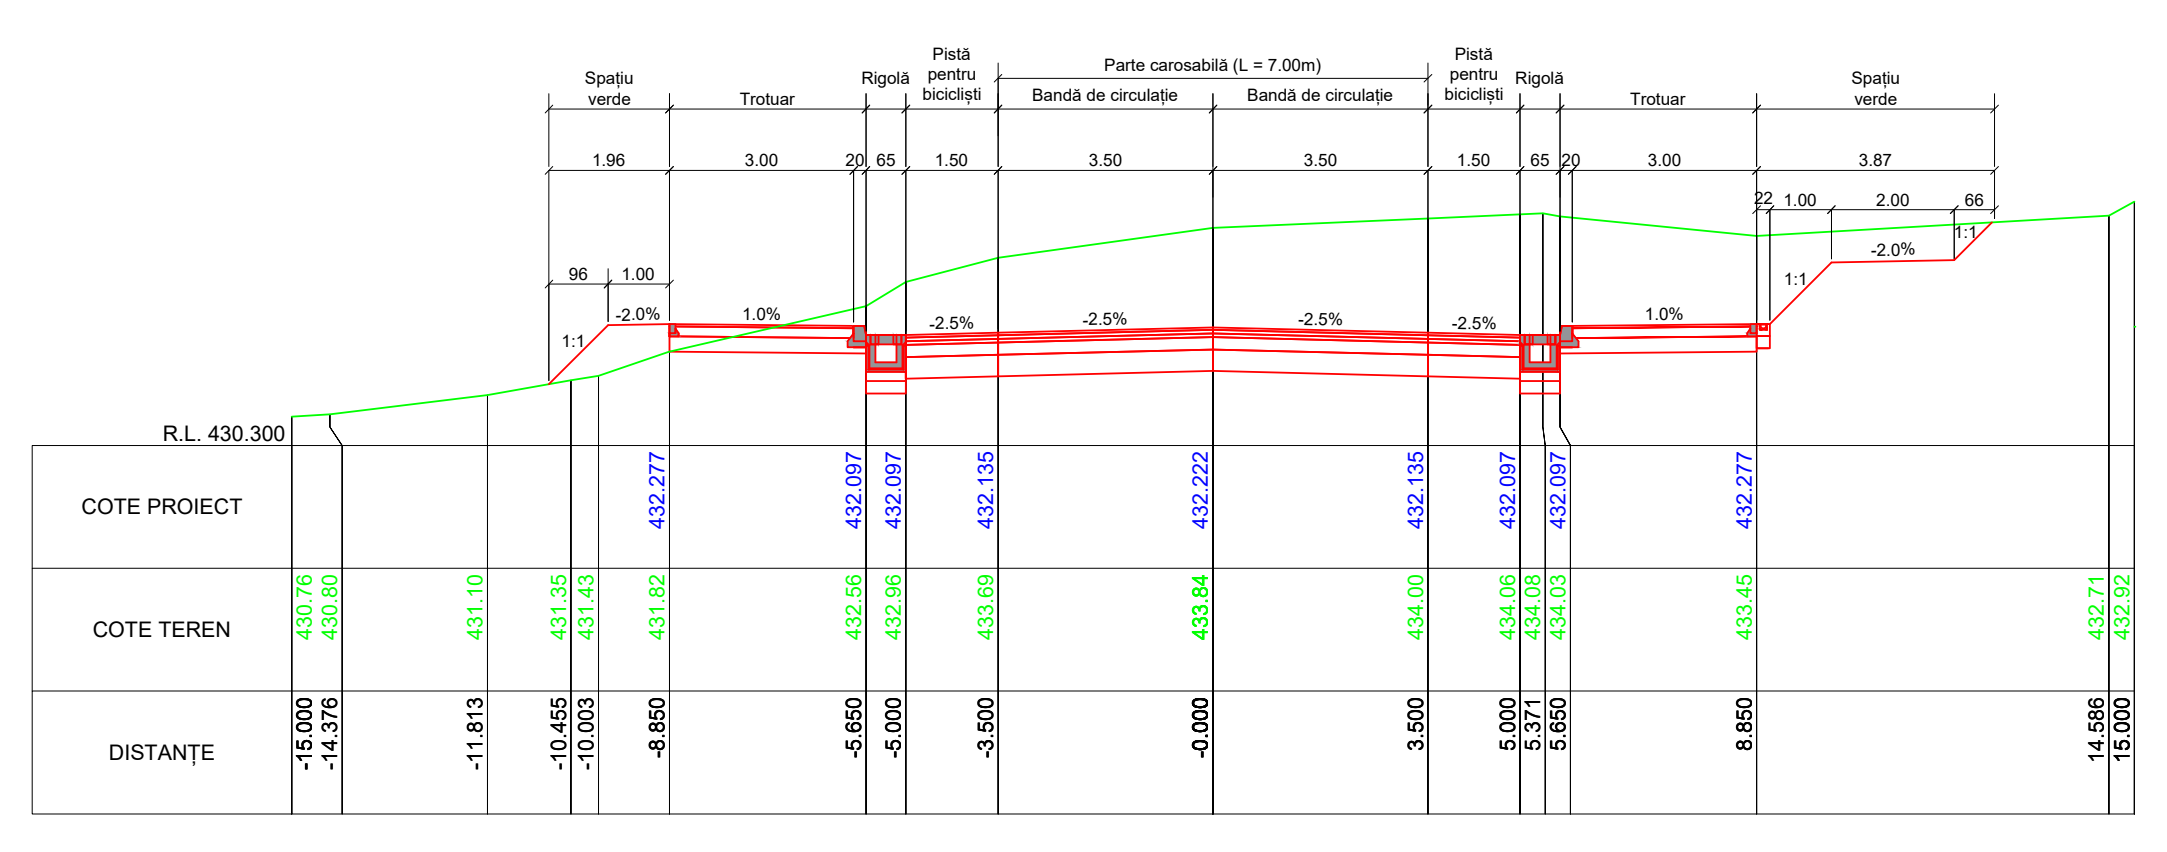
Km 60.000

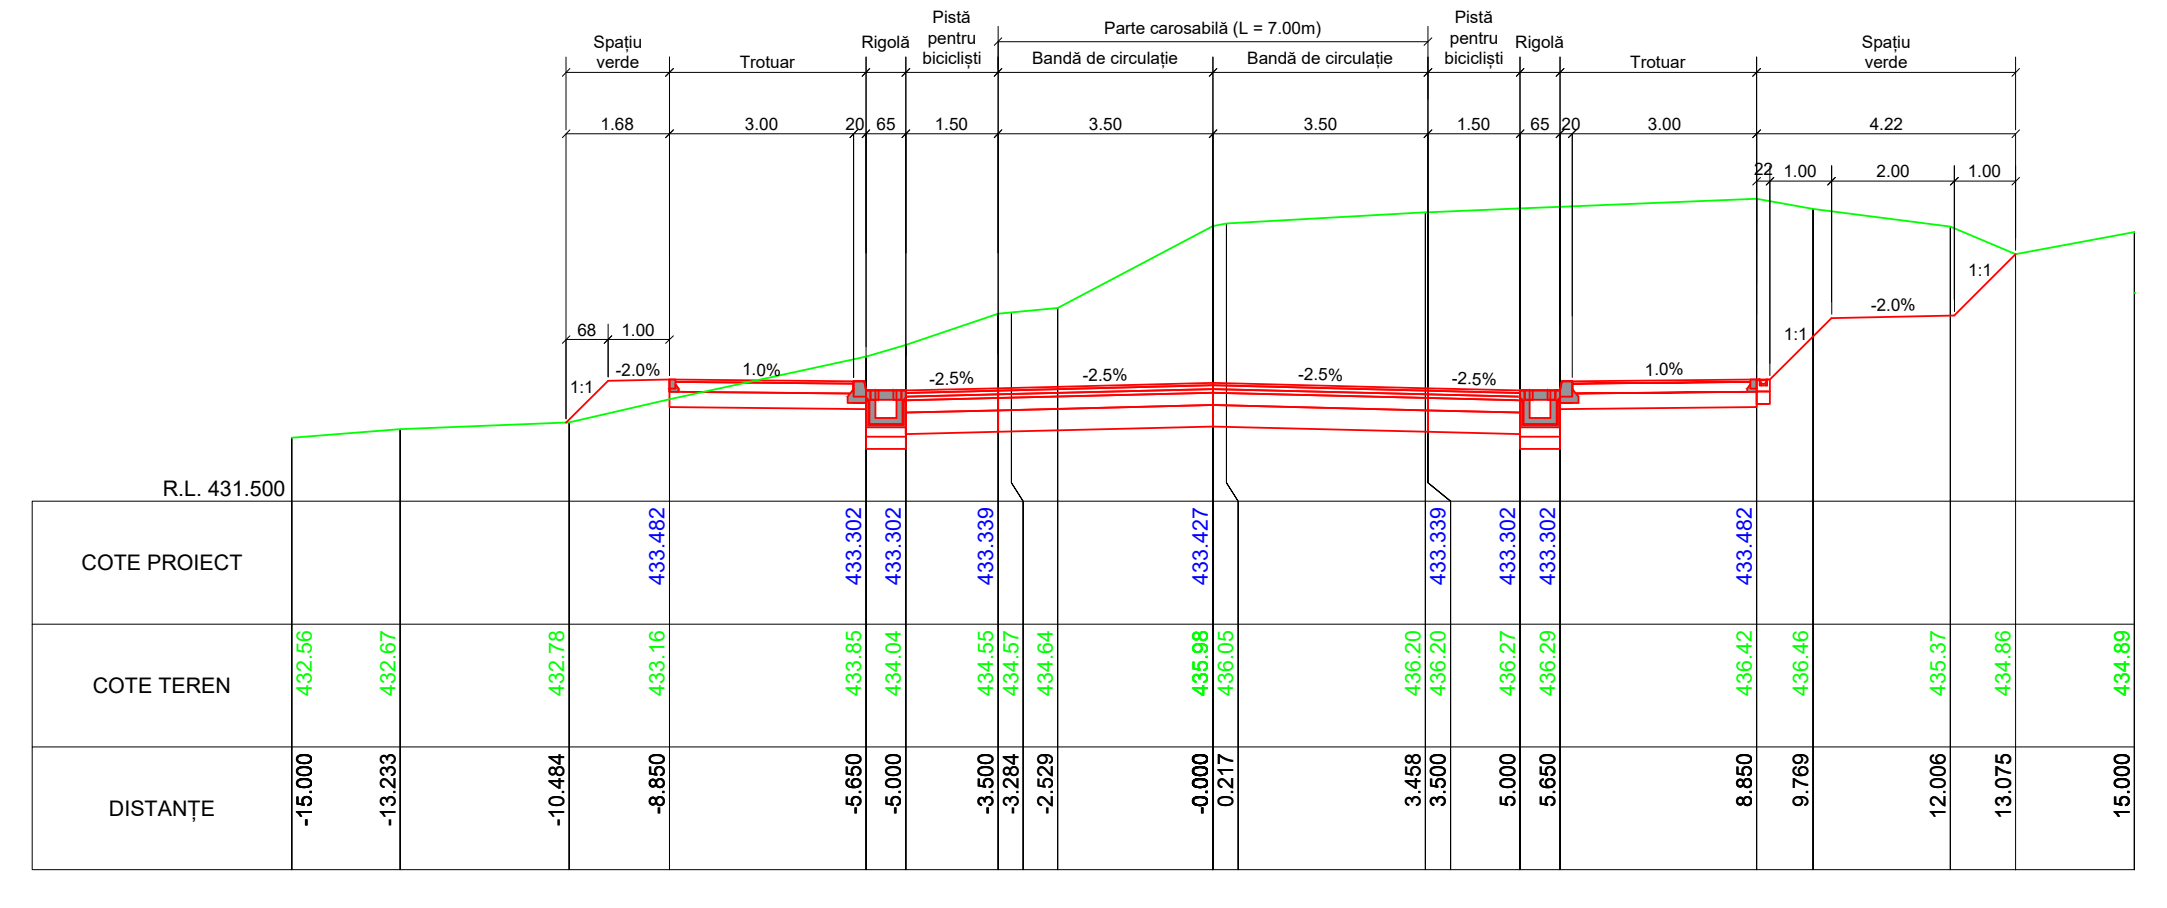
Km 90.000

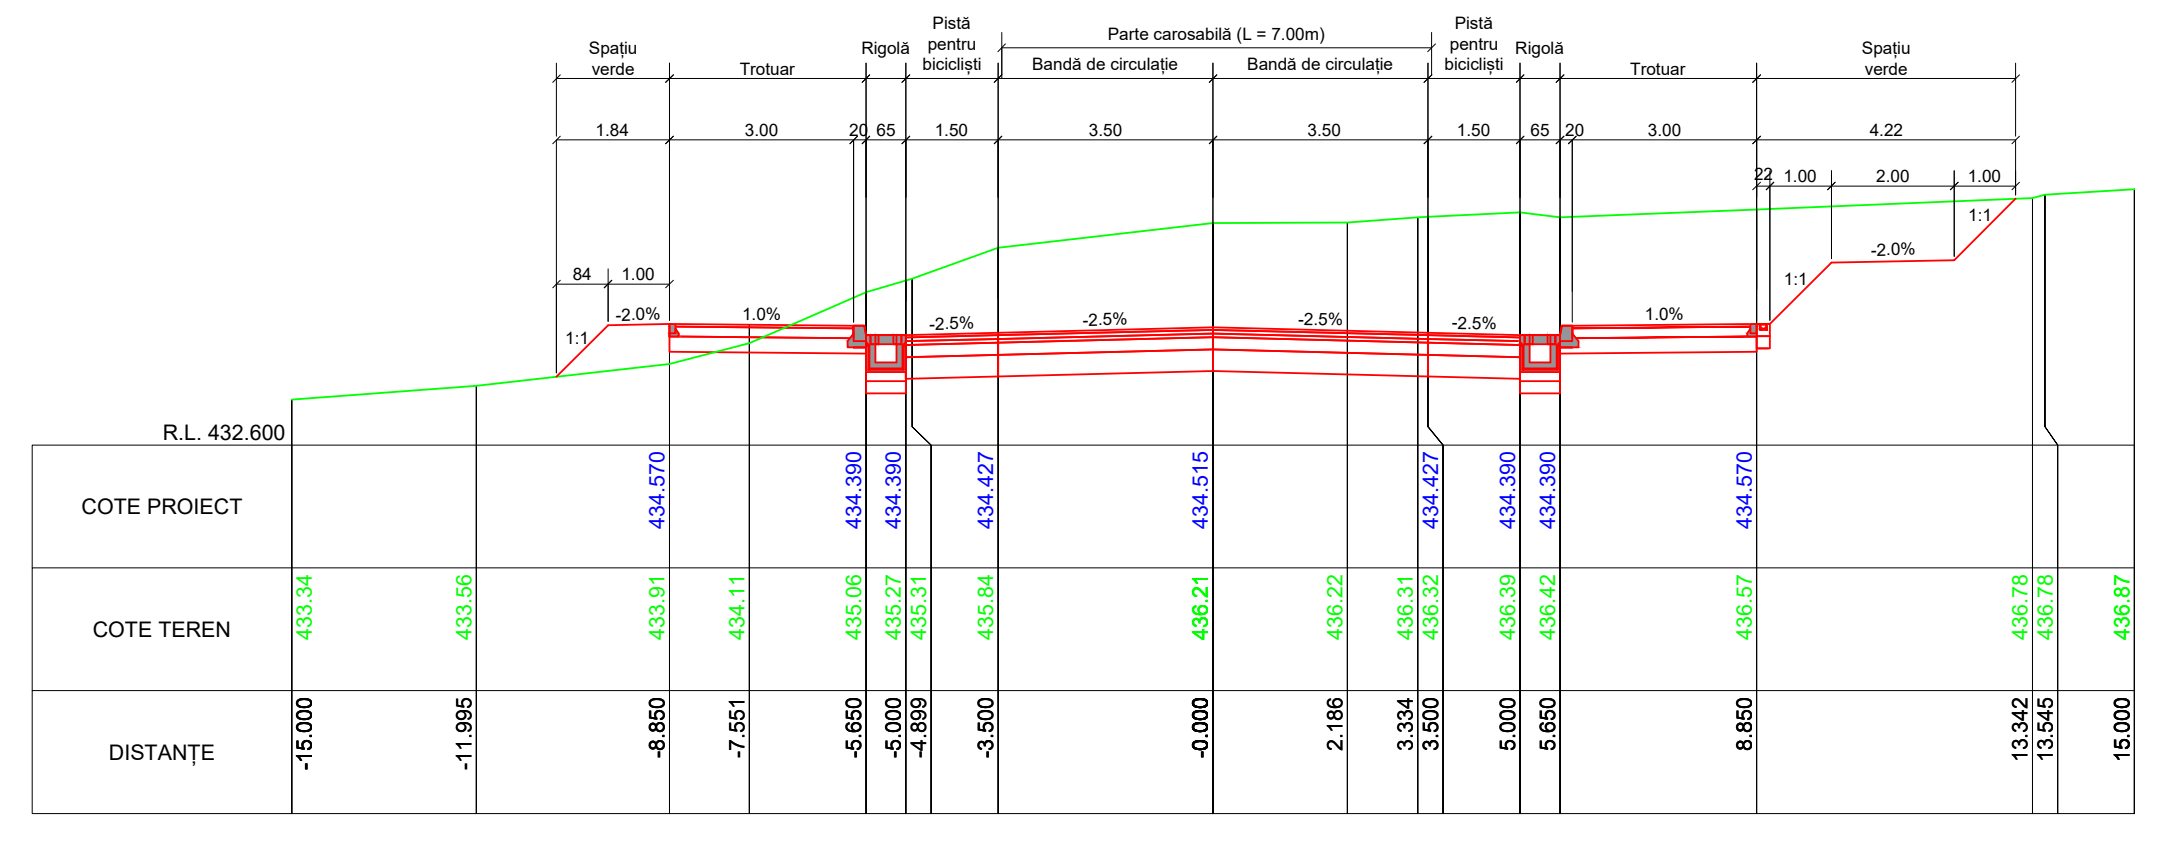
Km 120.000

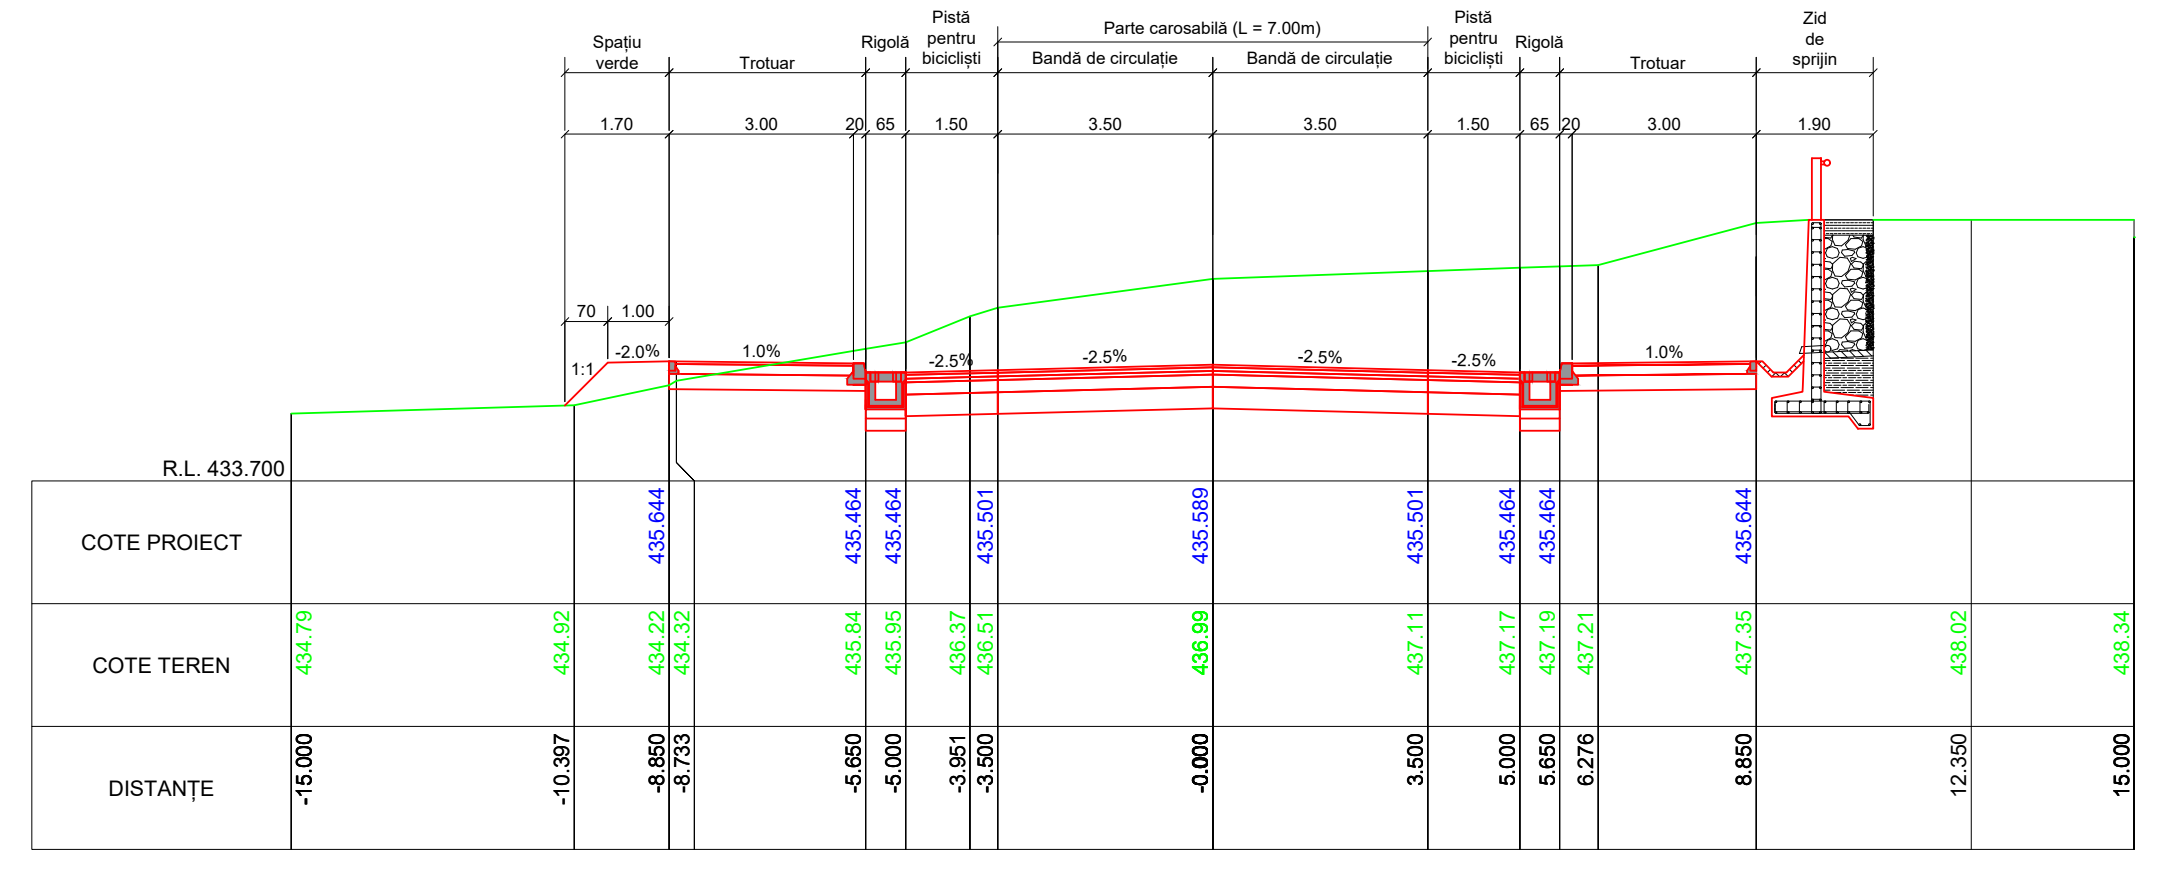
Km 140.000

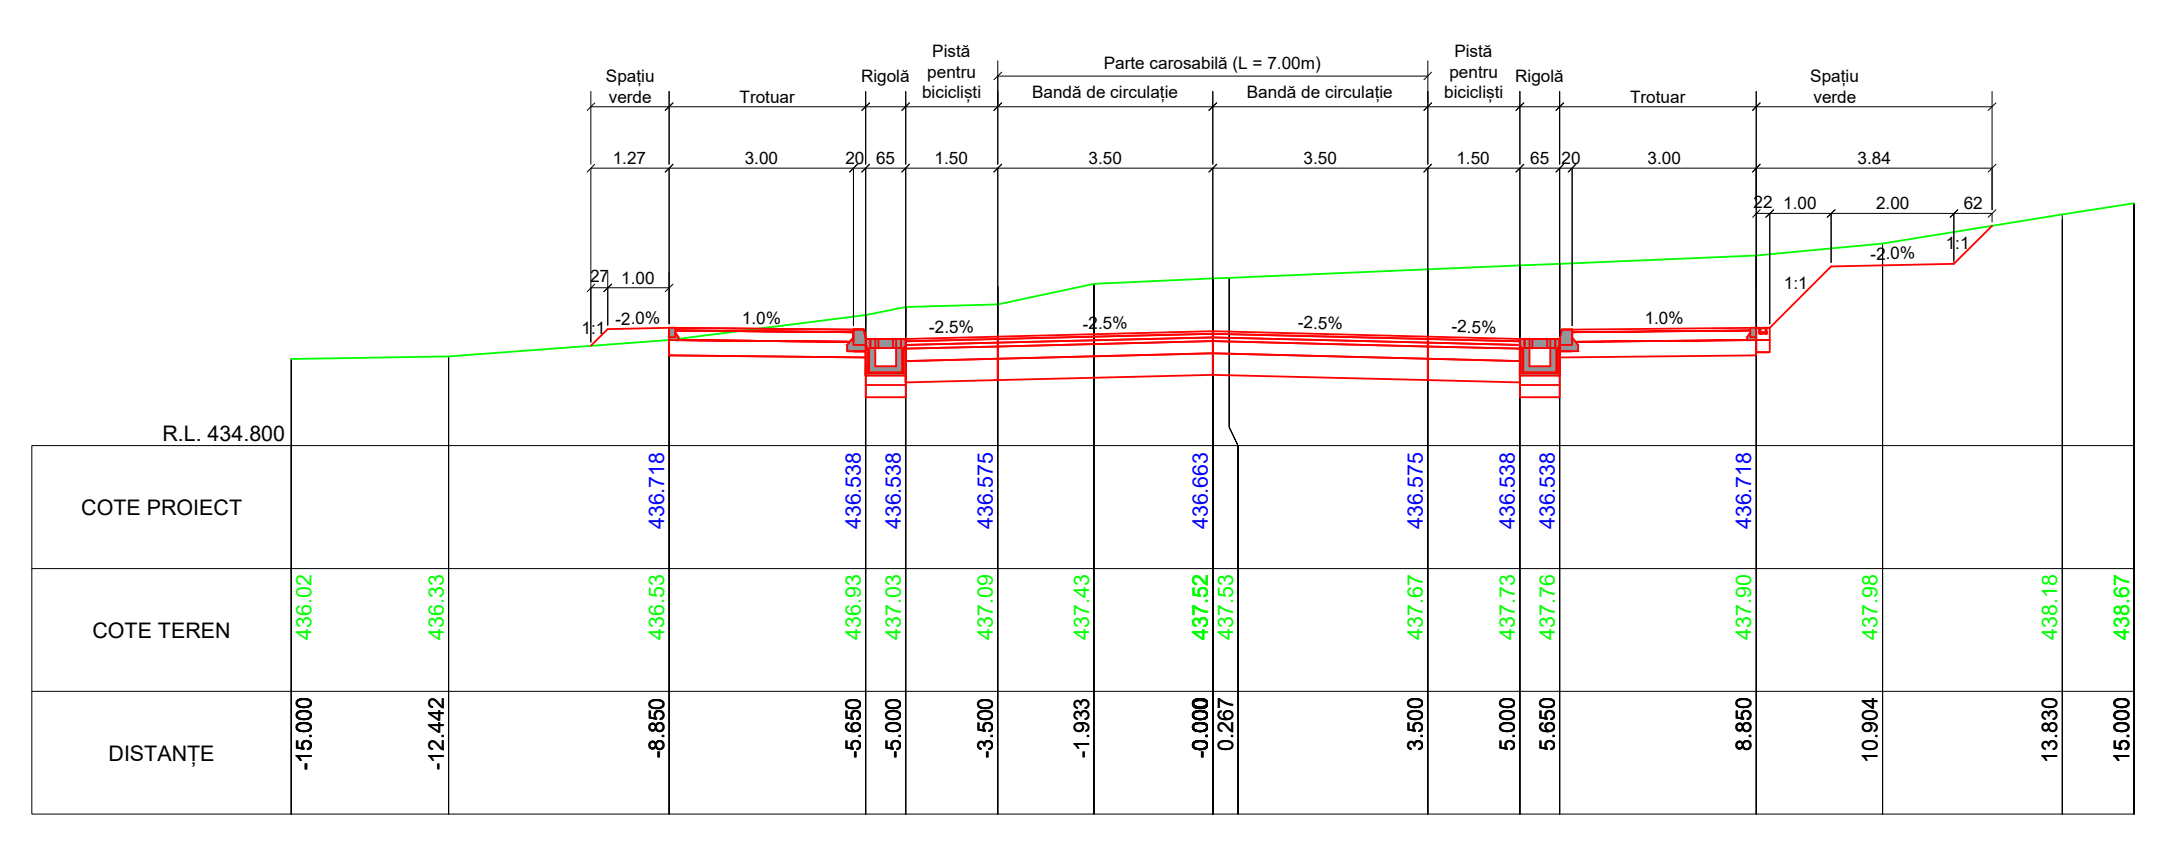
Km 190.000

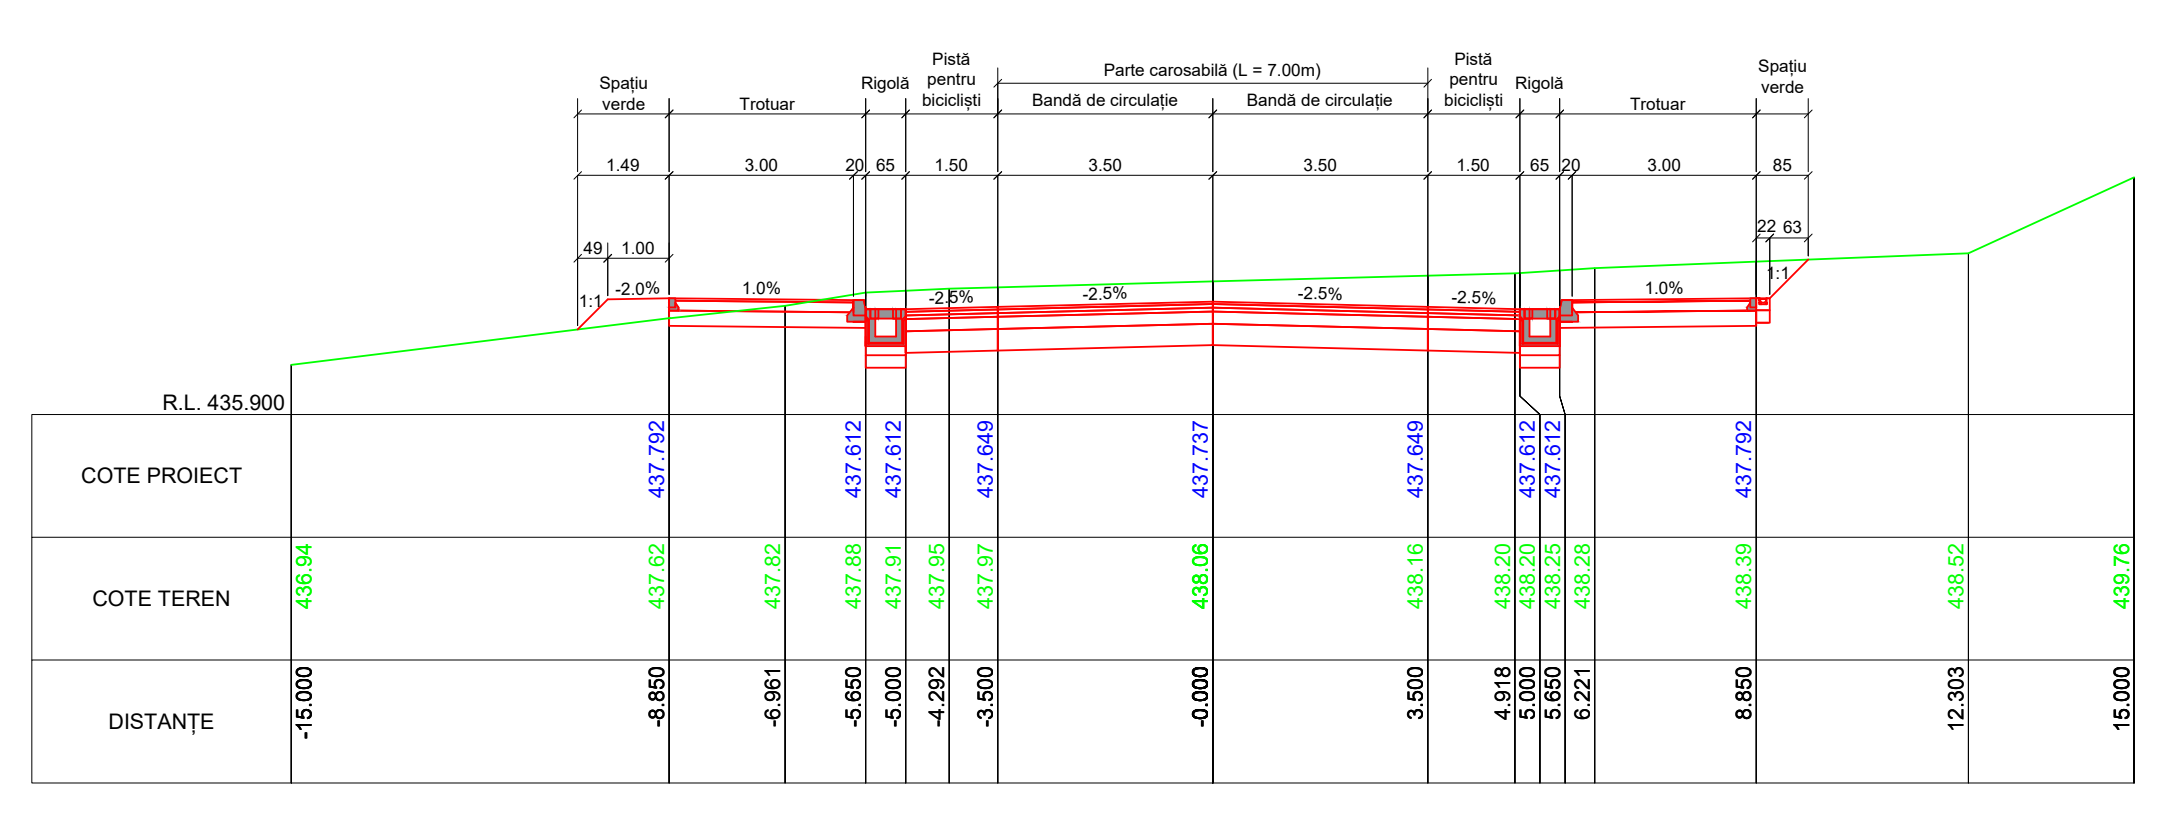
Km 210.000

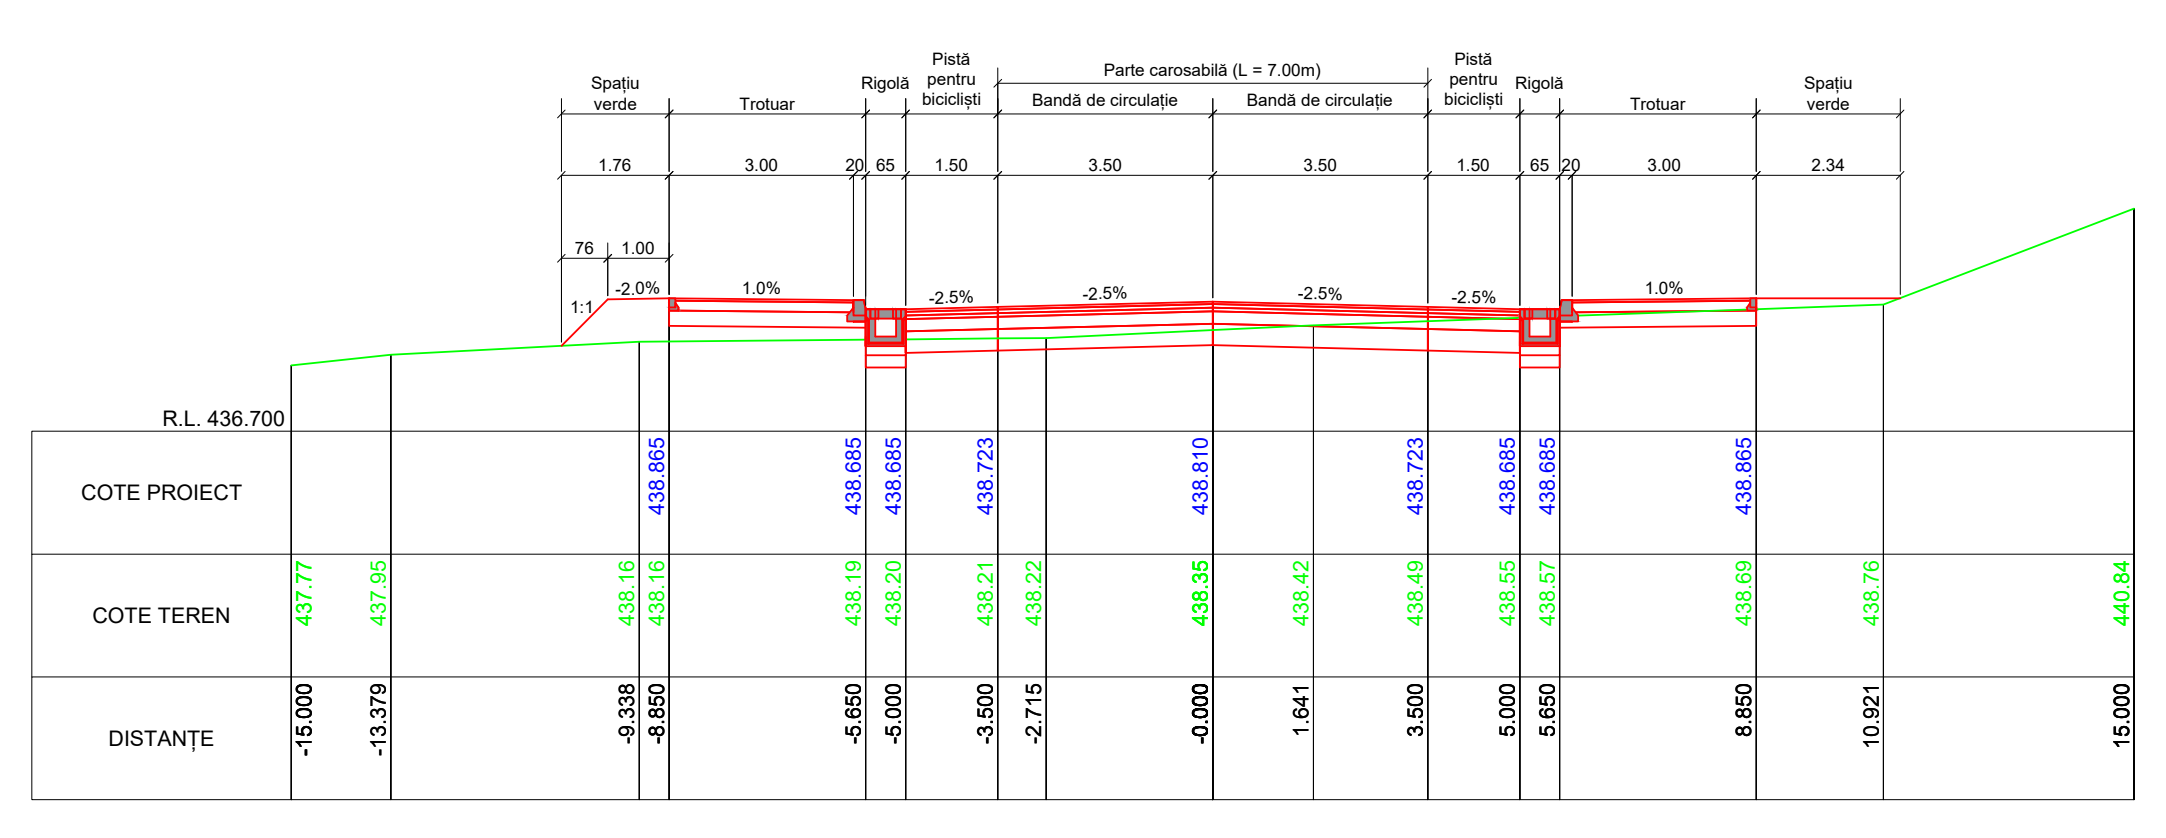
Km 240.000

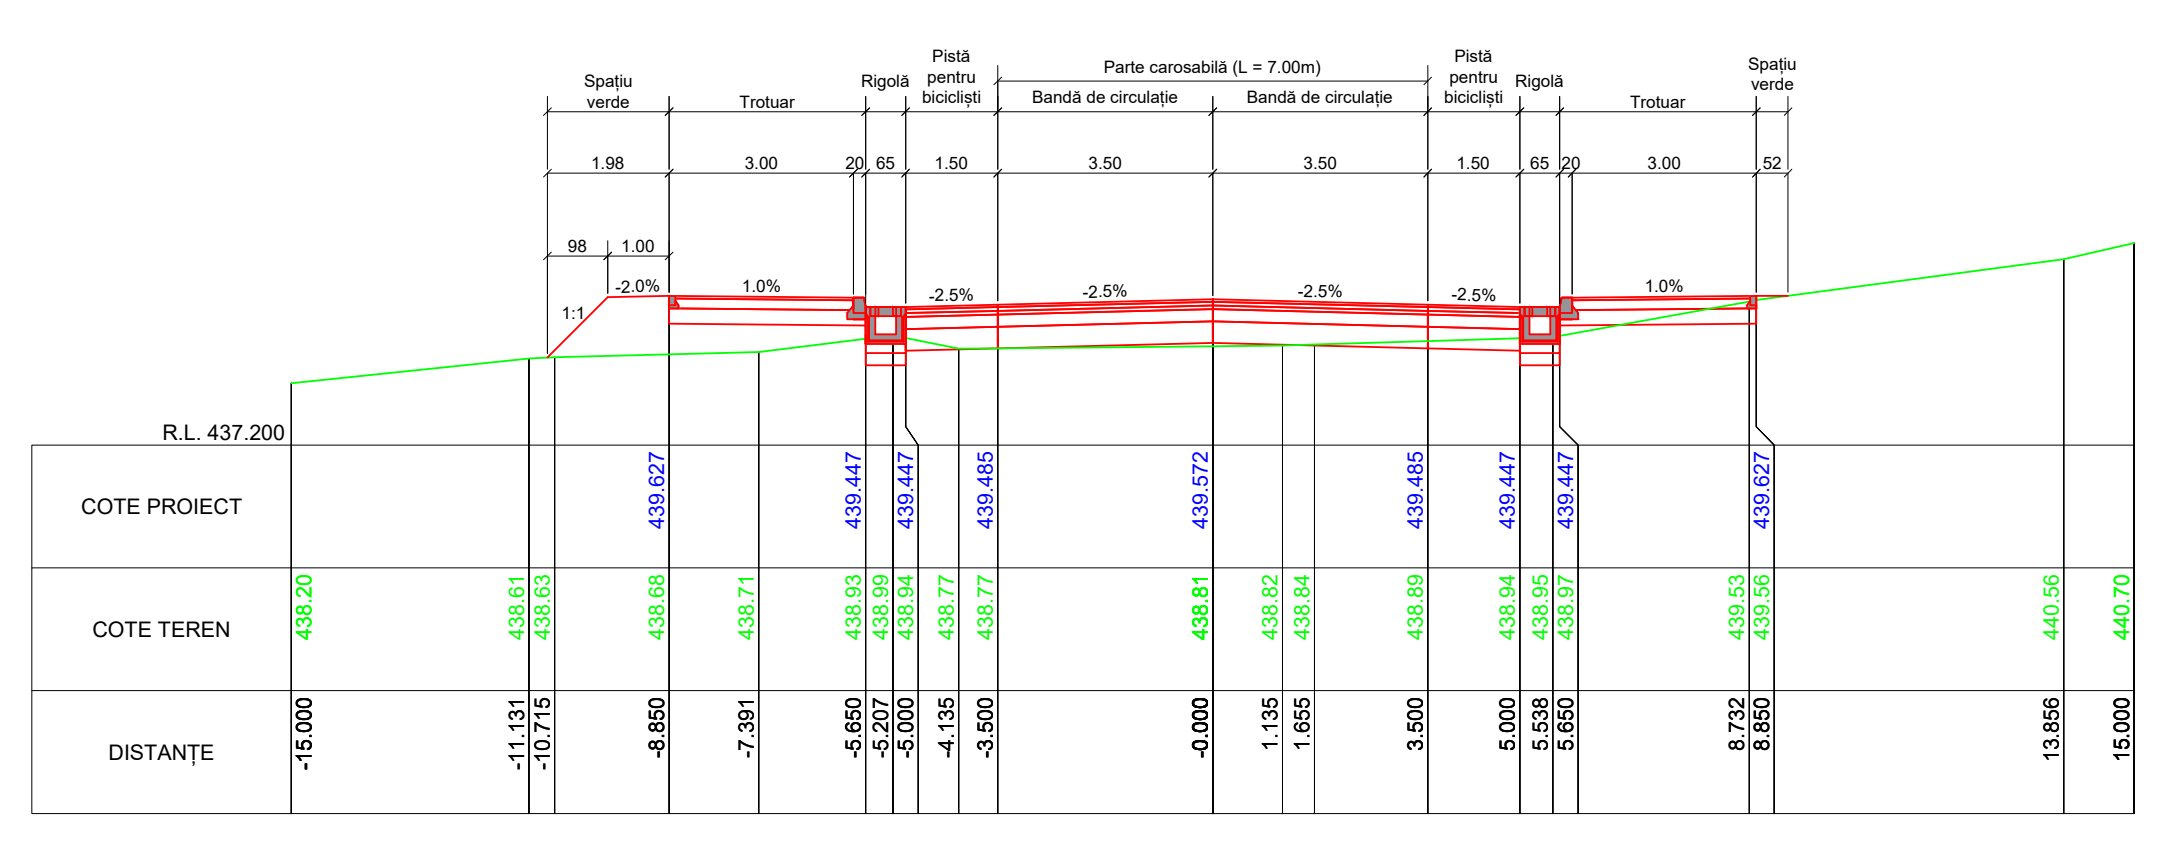
Km 270.000

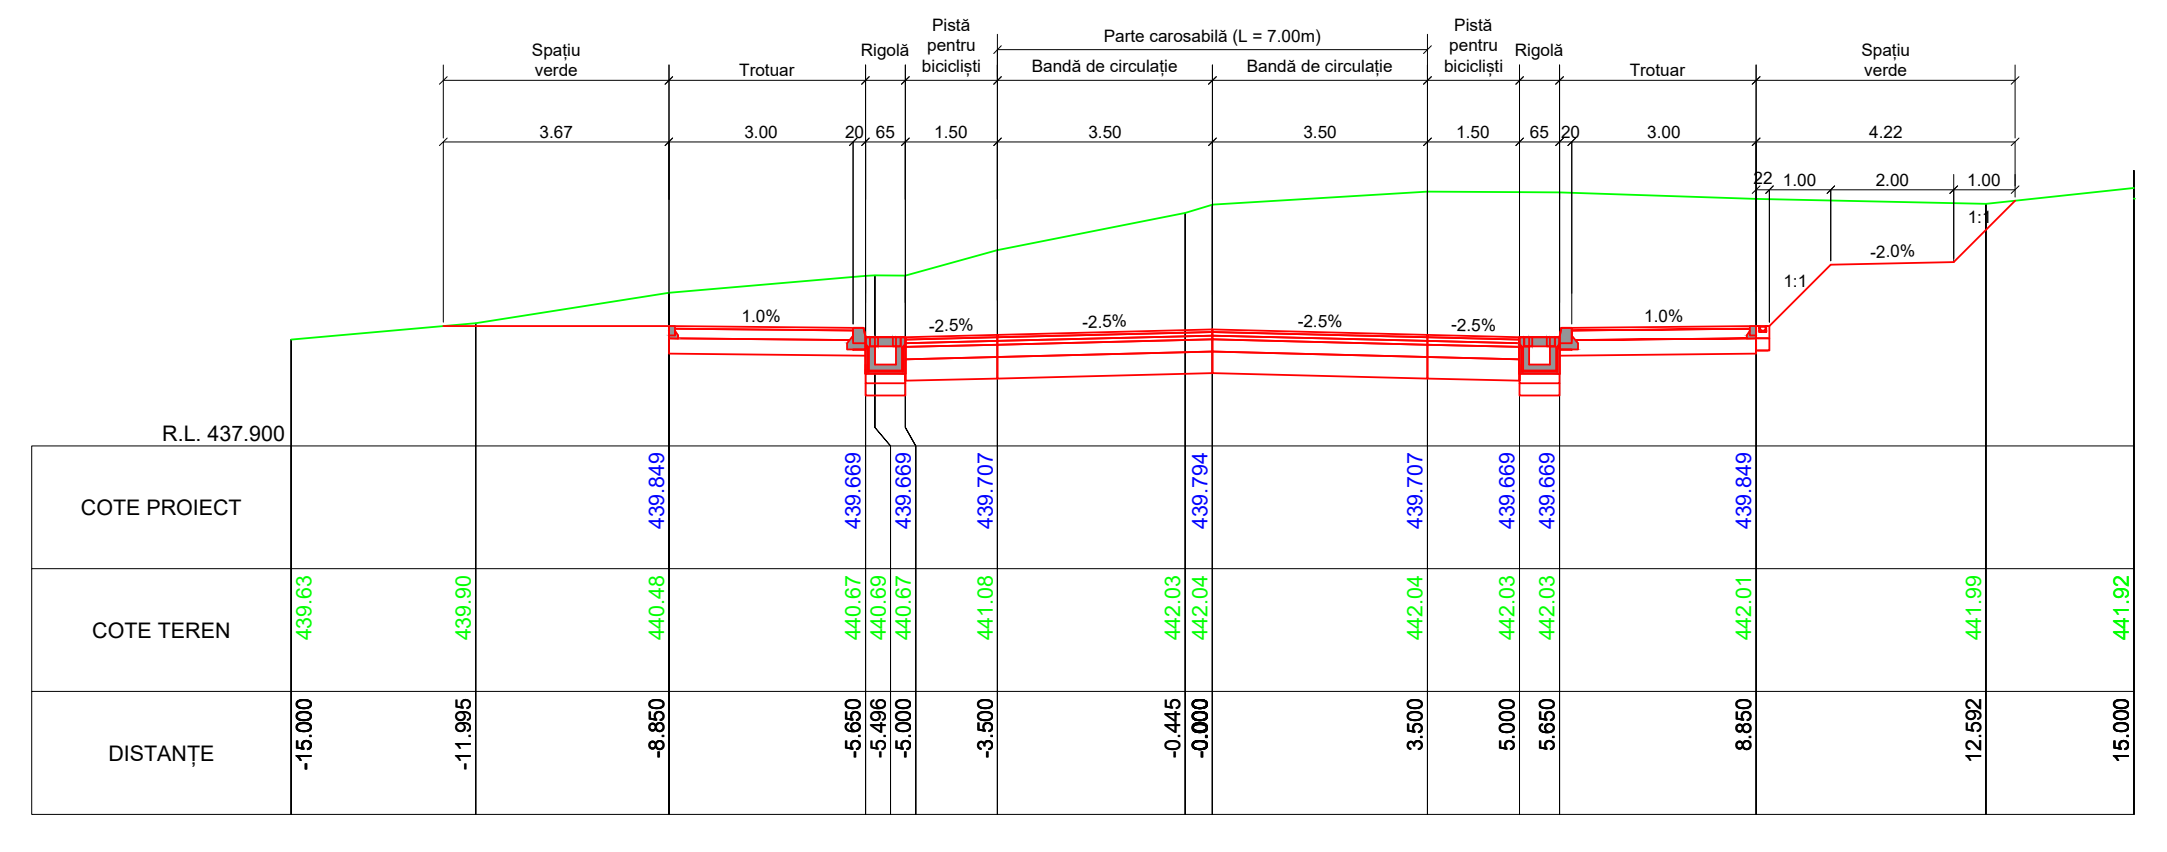
Km 300.000

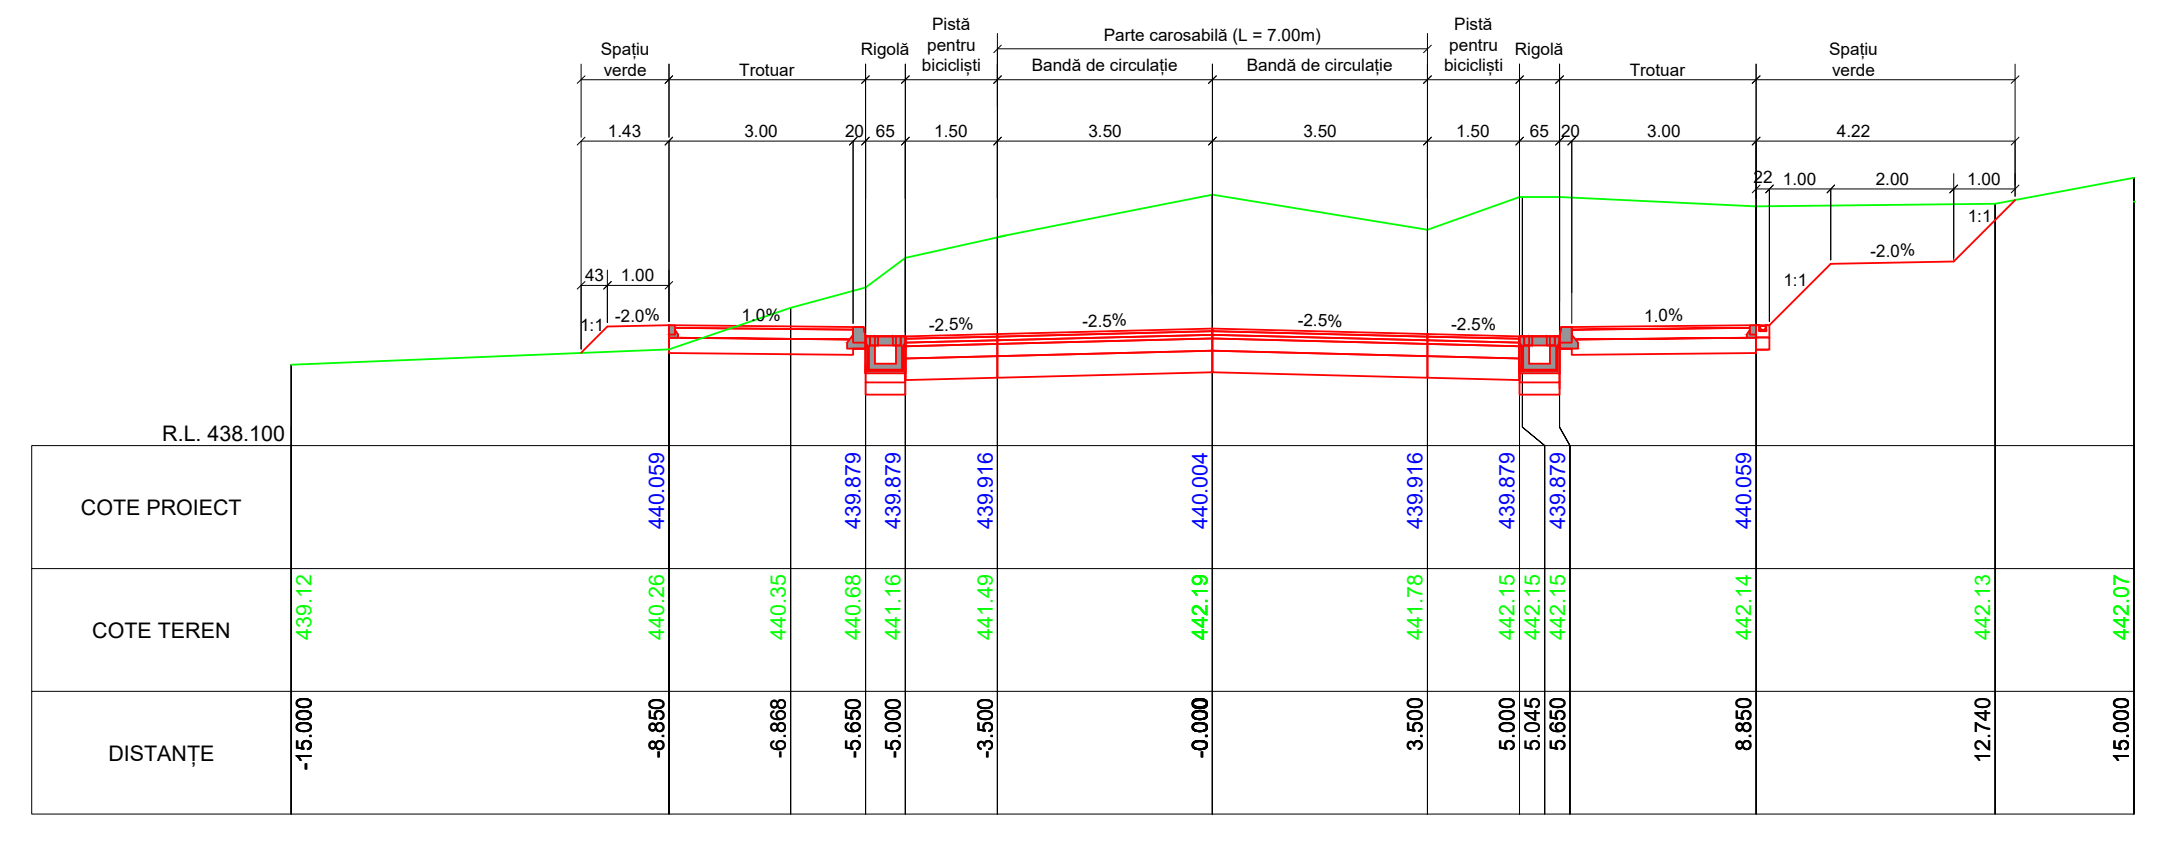
Km 330.000

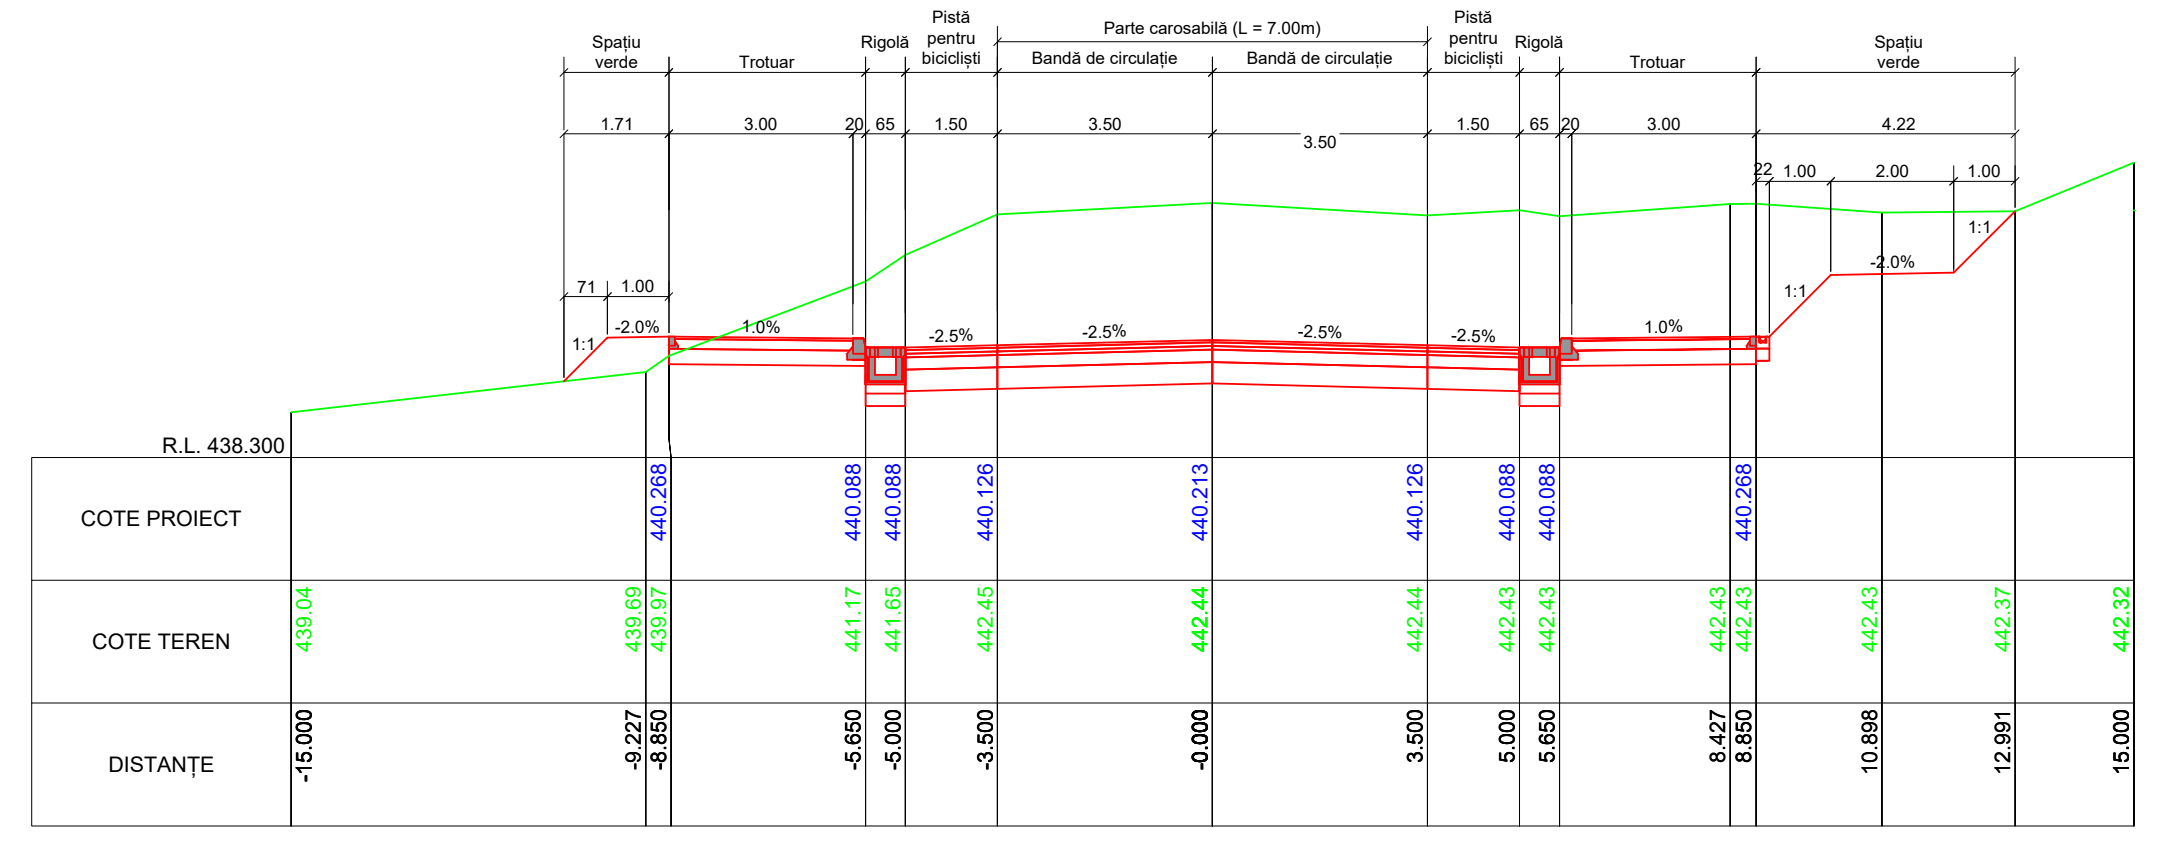
Km 360.000

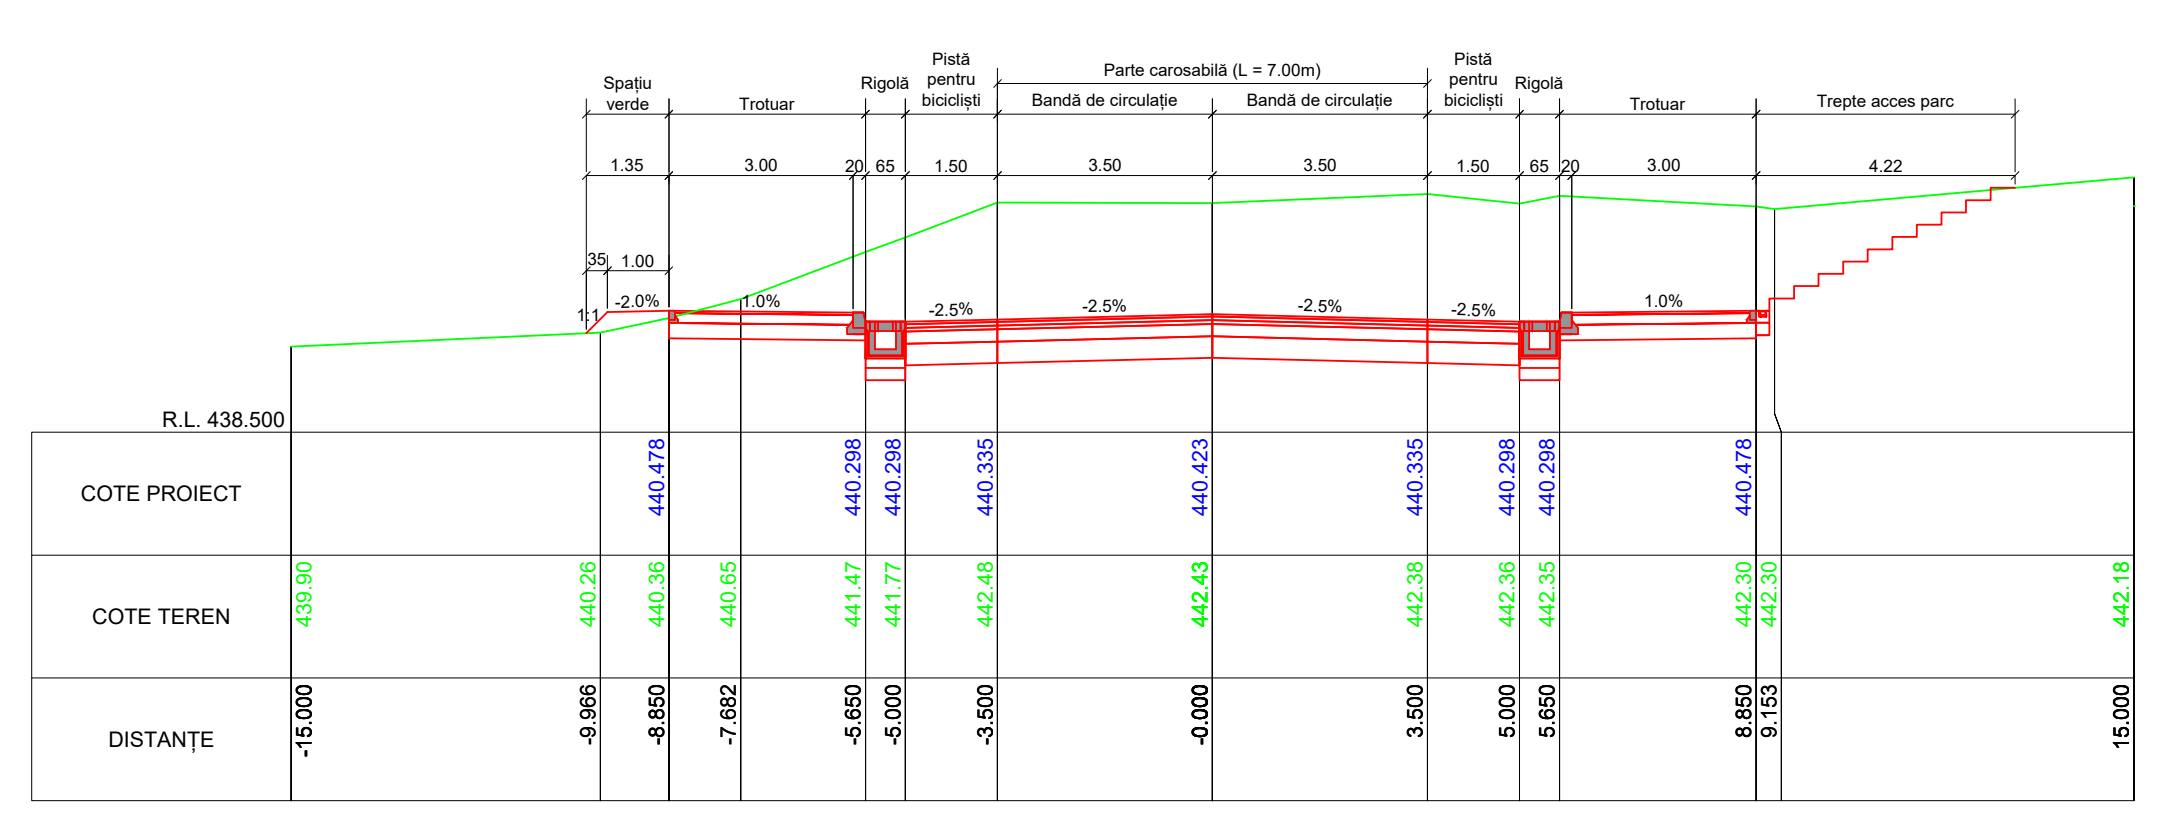
Km 390.000

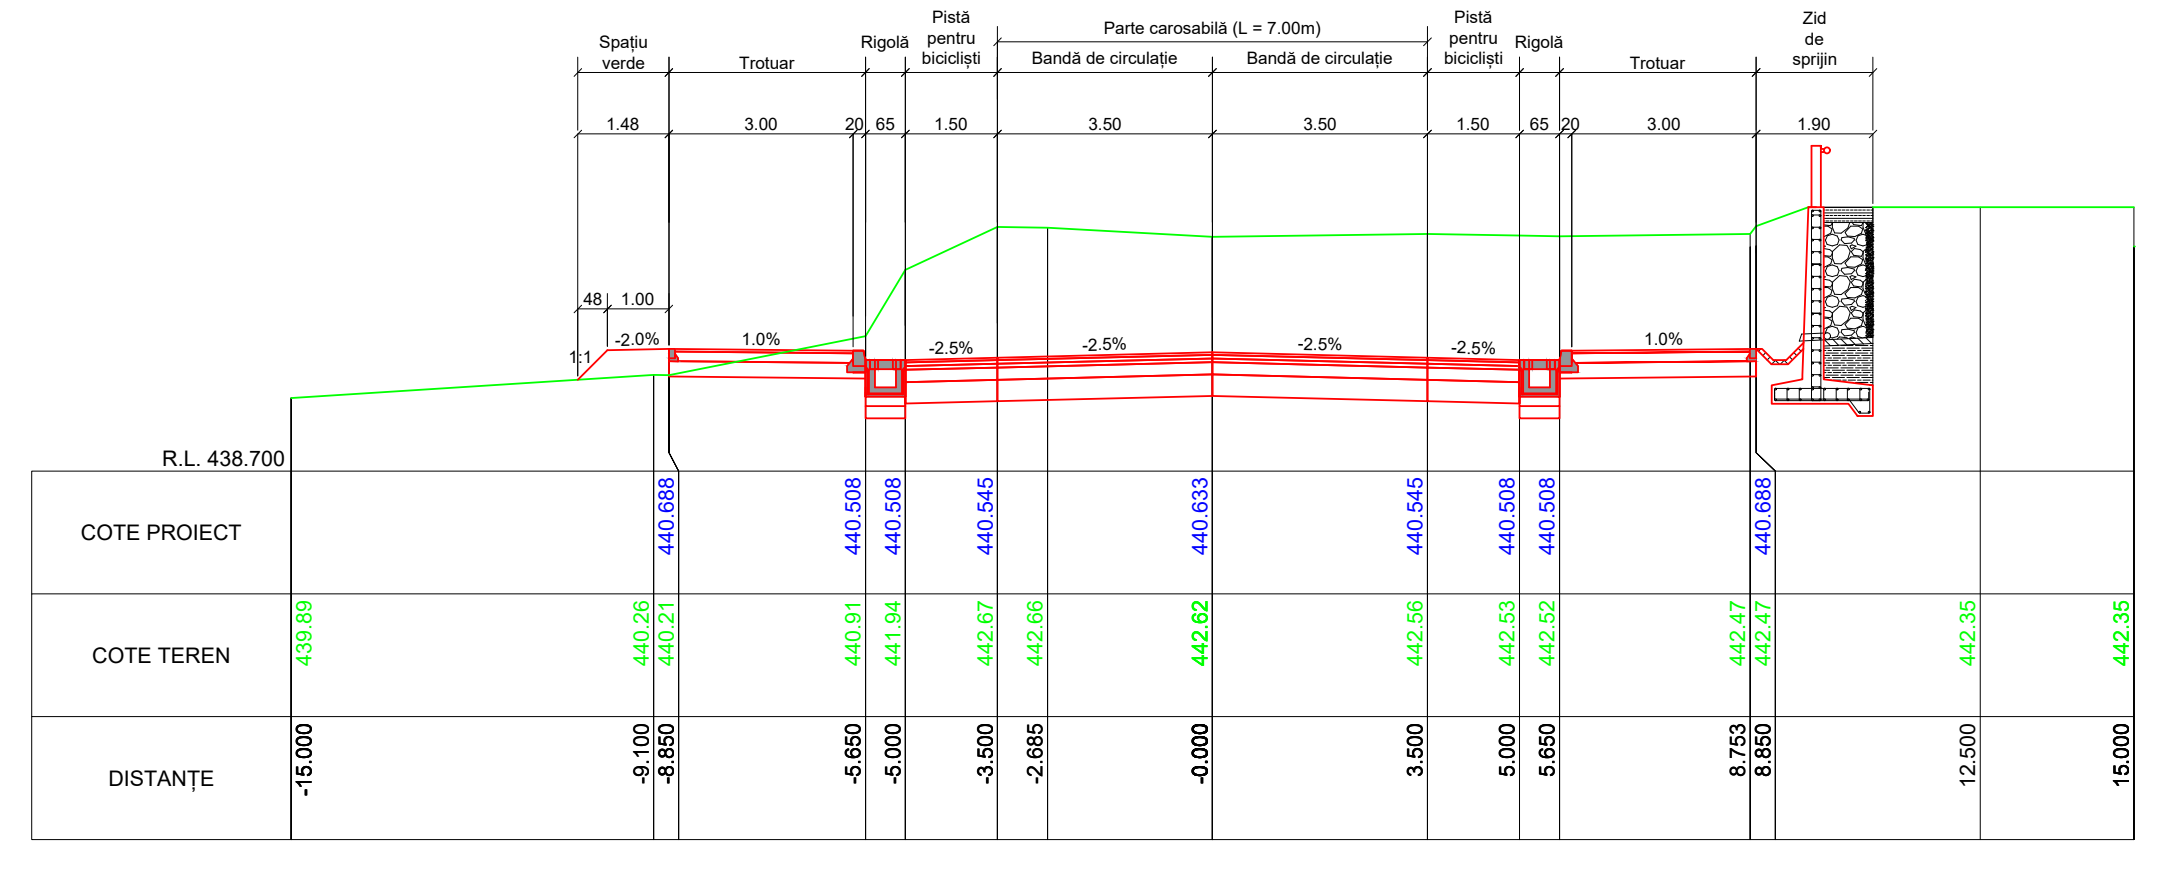
Km 410.000

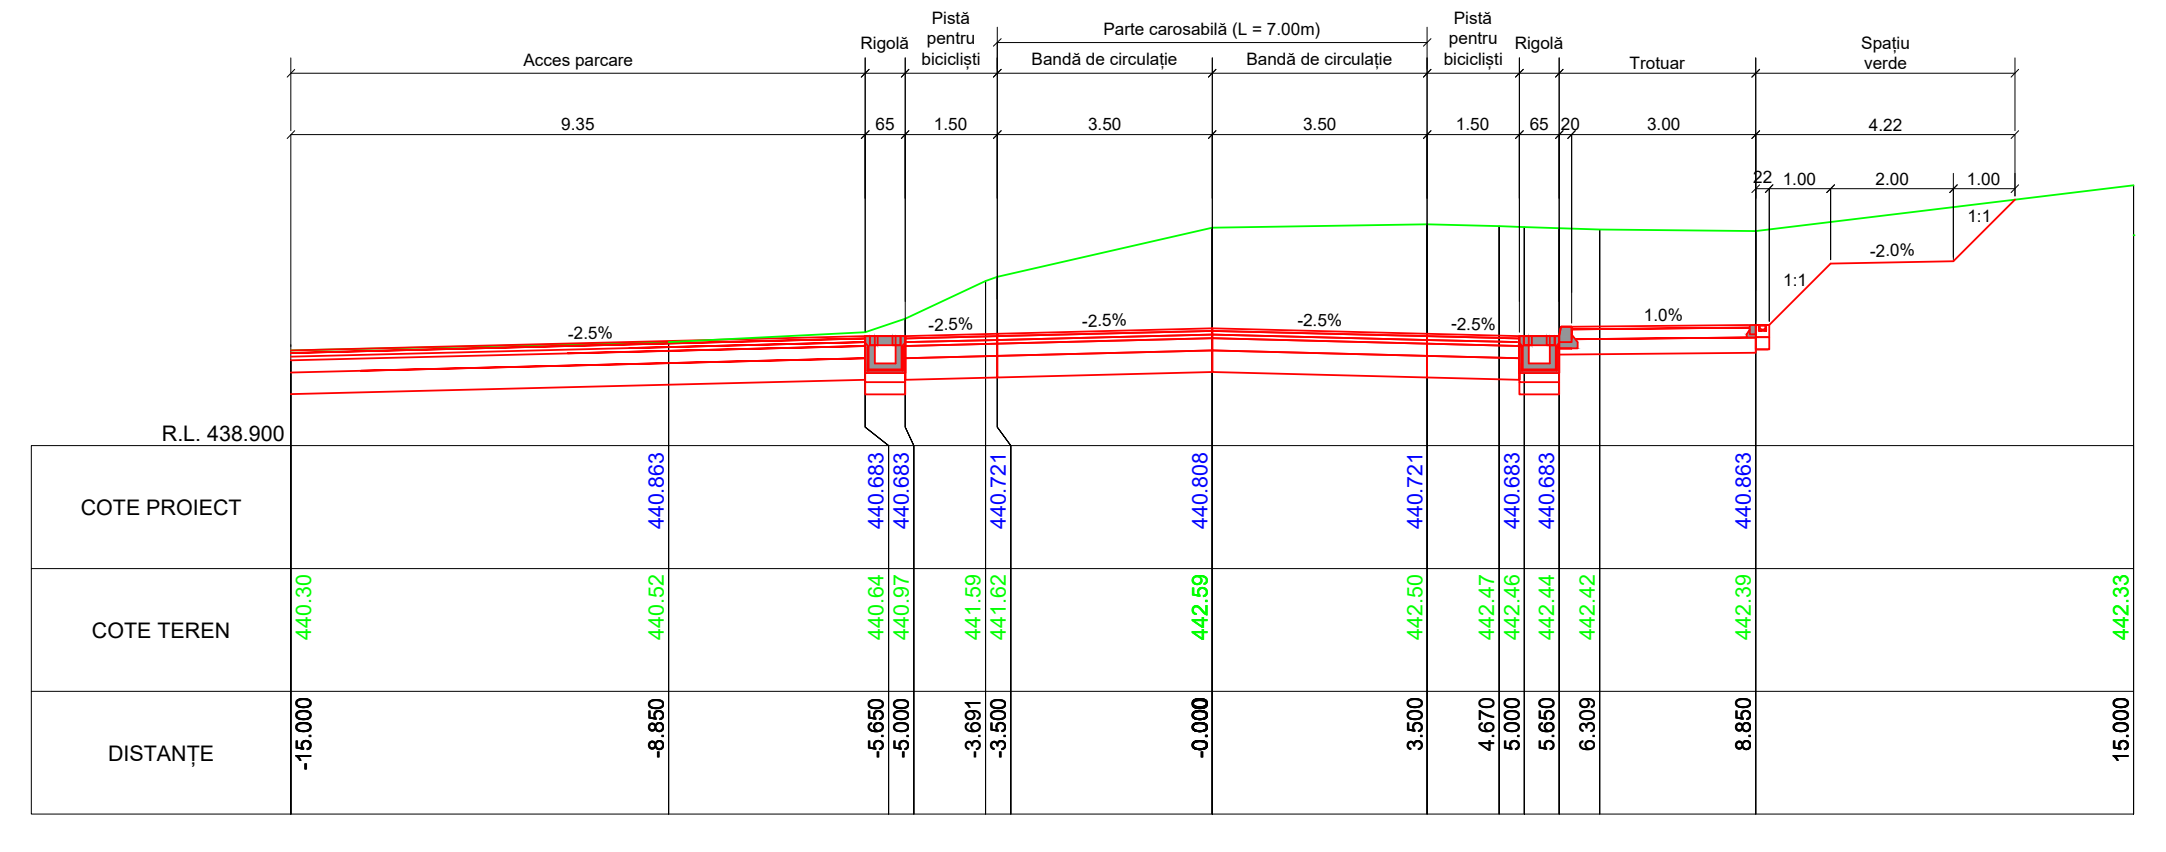
Km 450.000

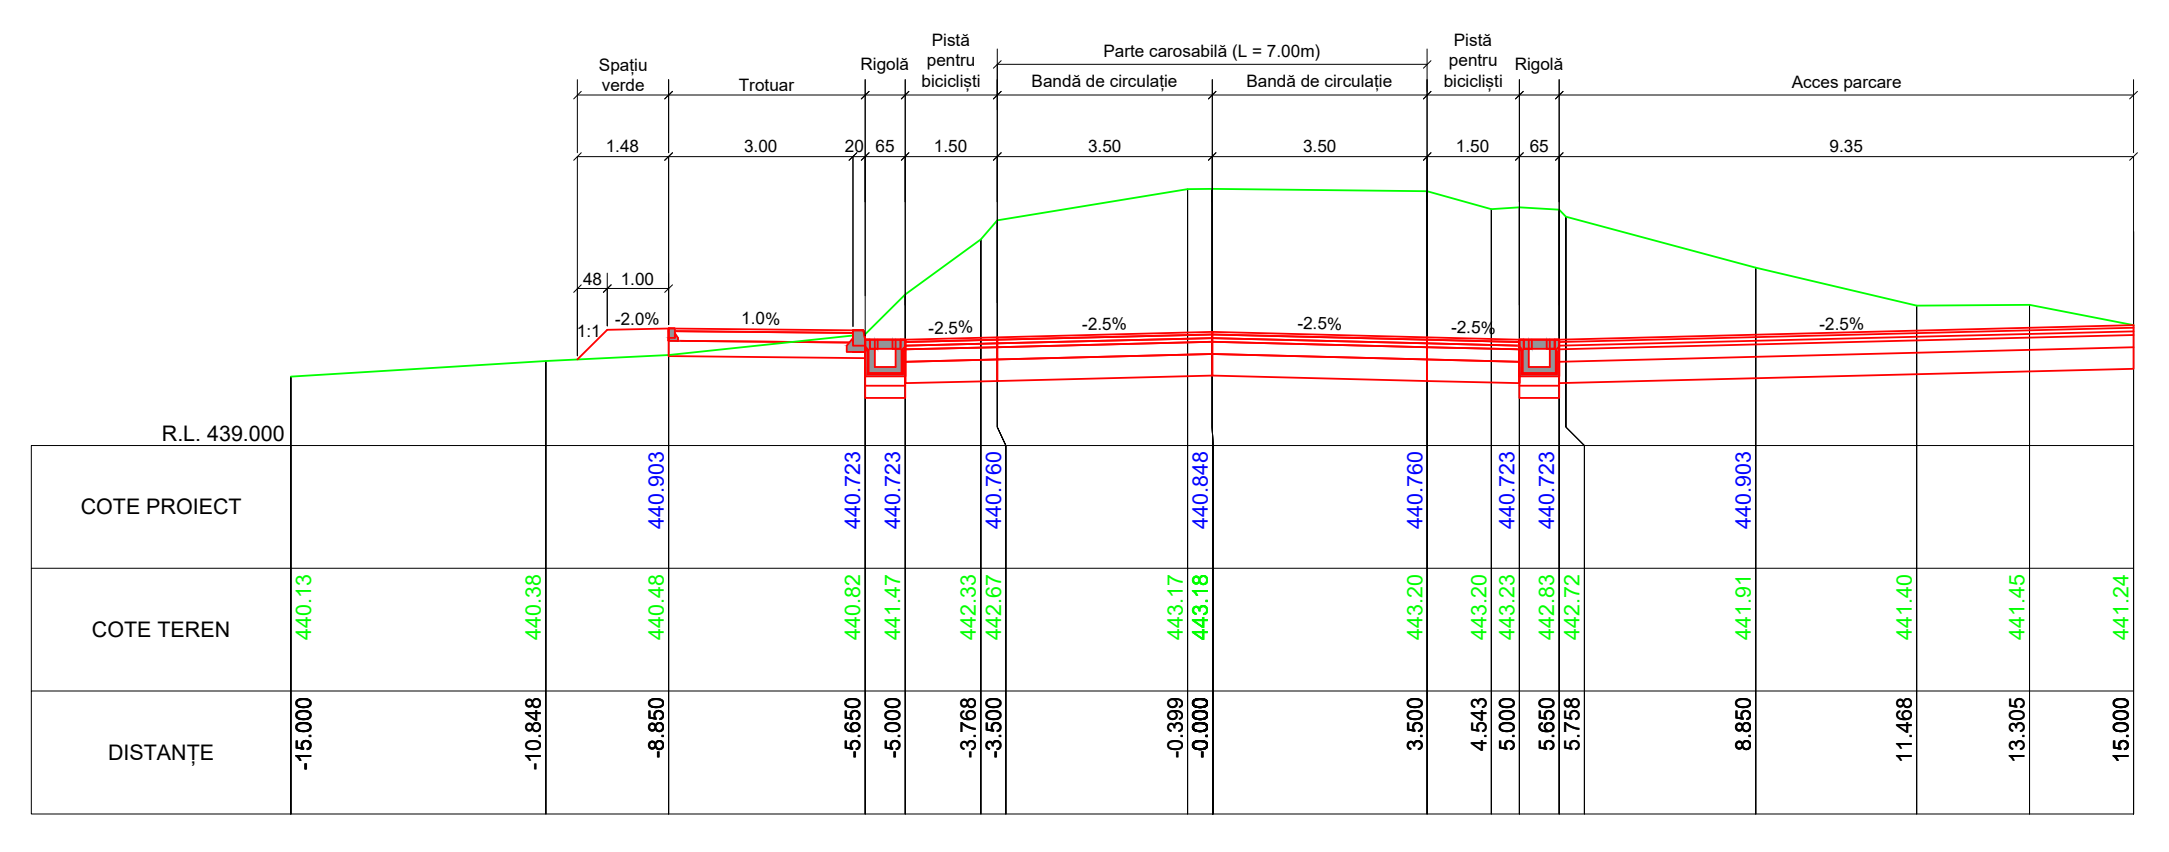
Km 480.000

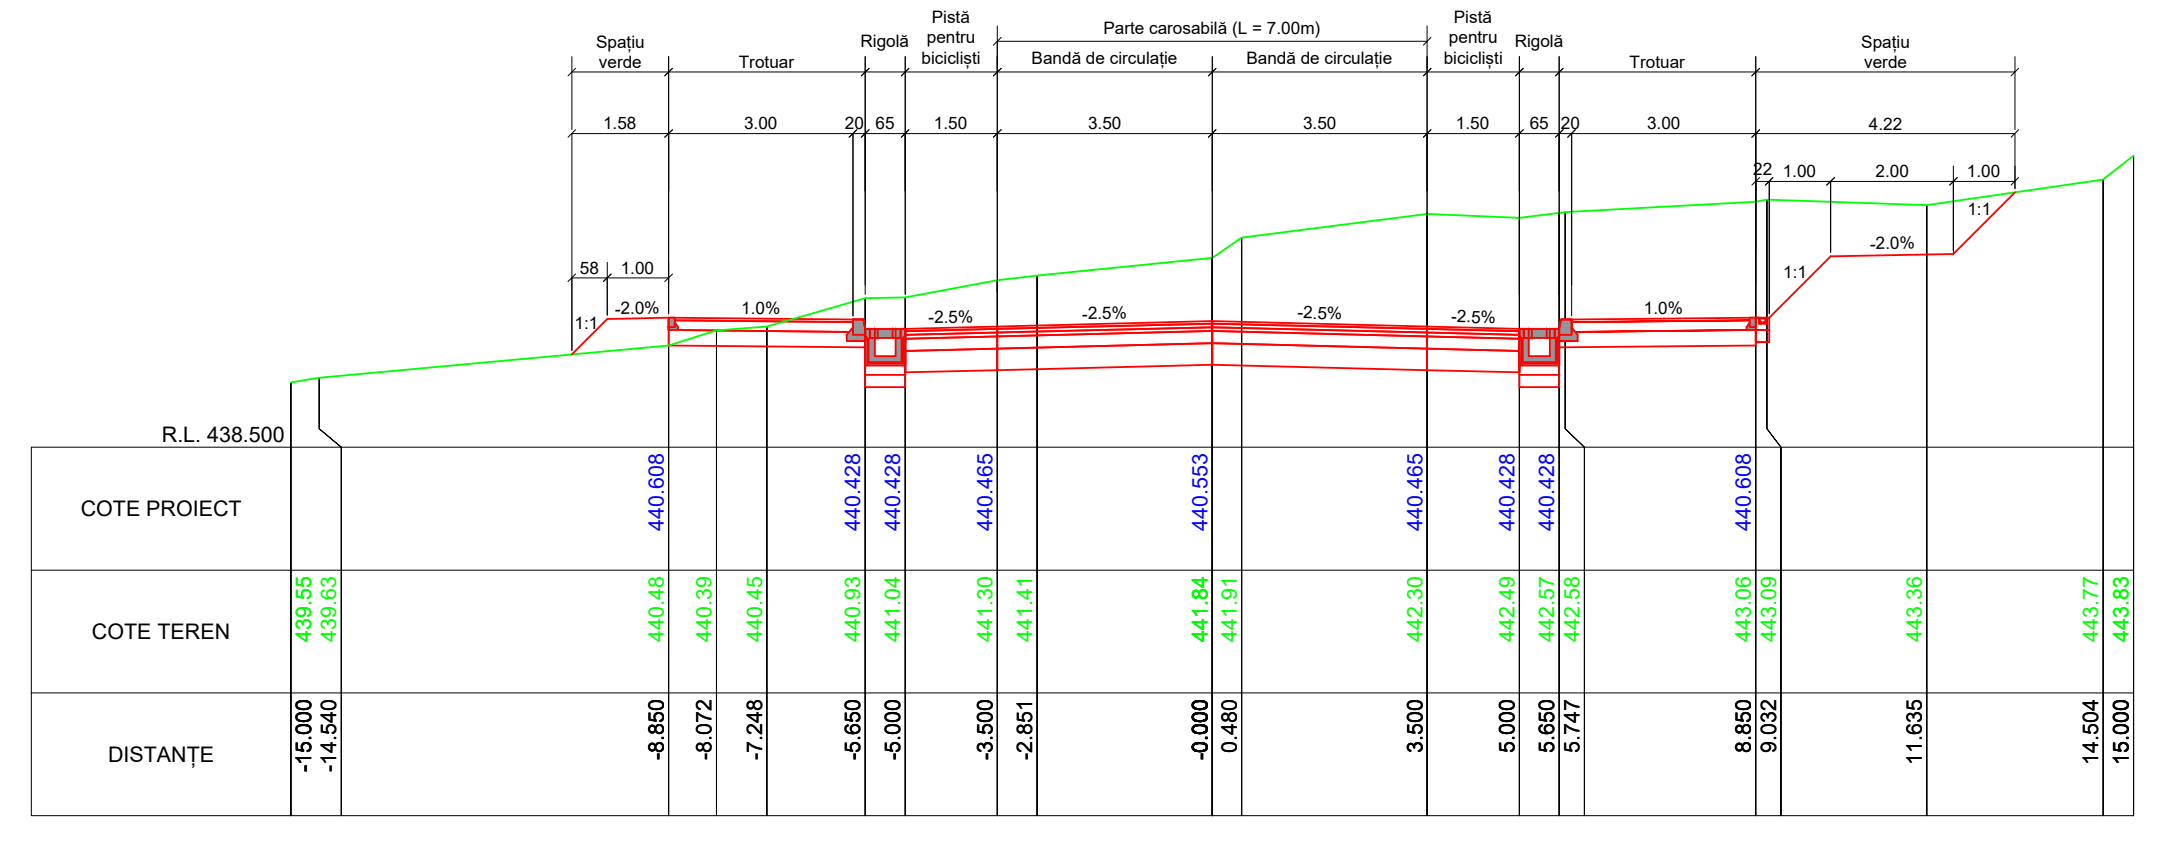
Km 510.000

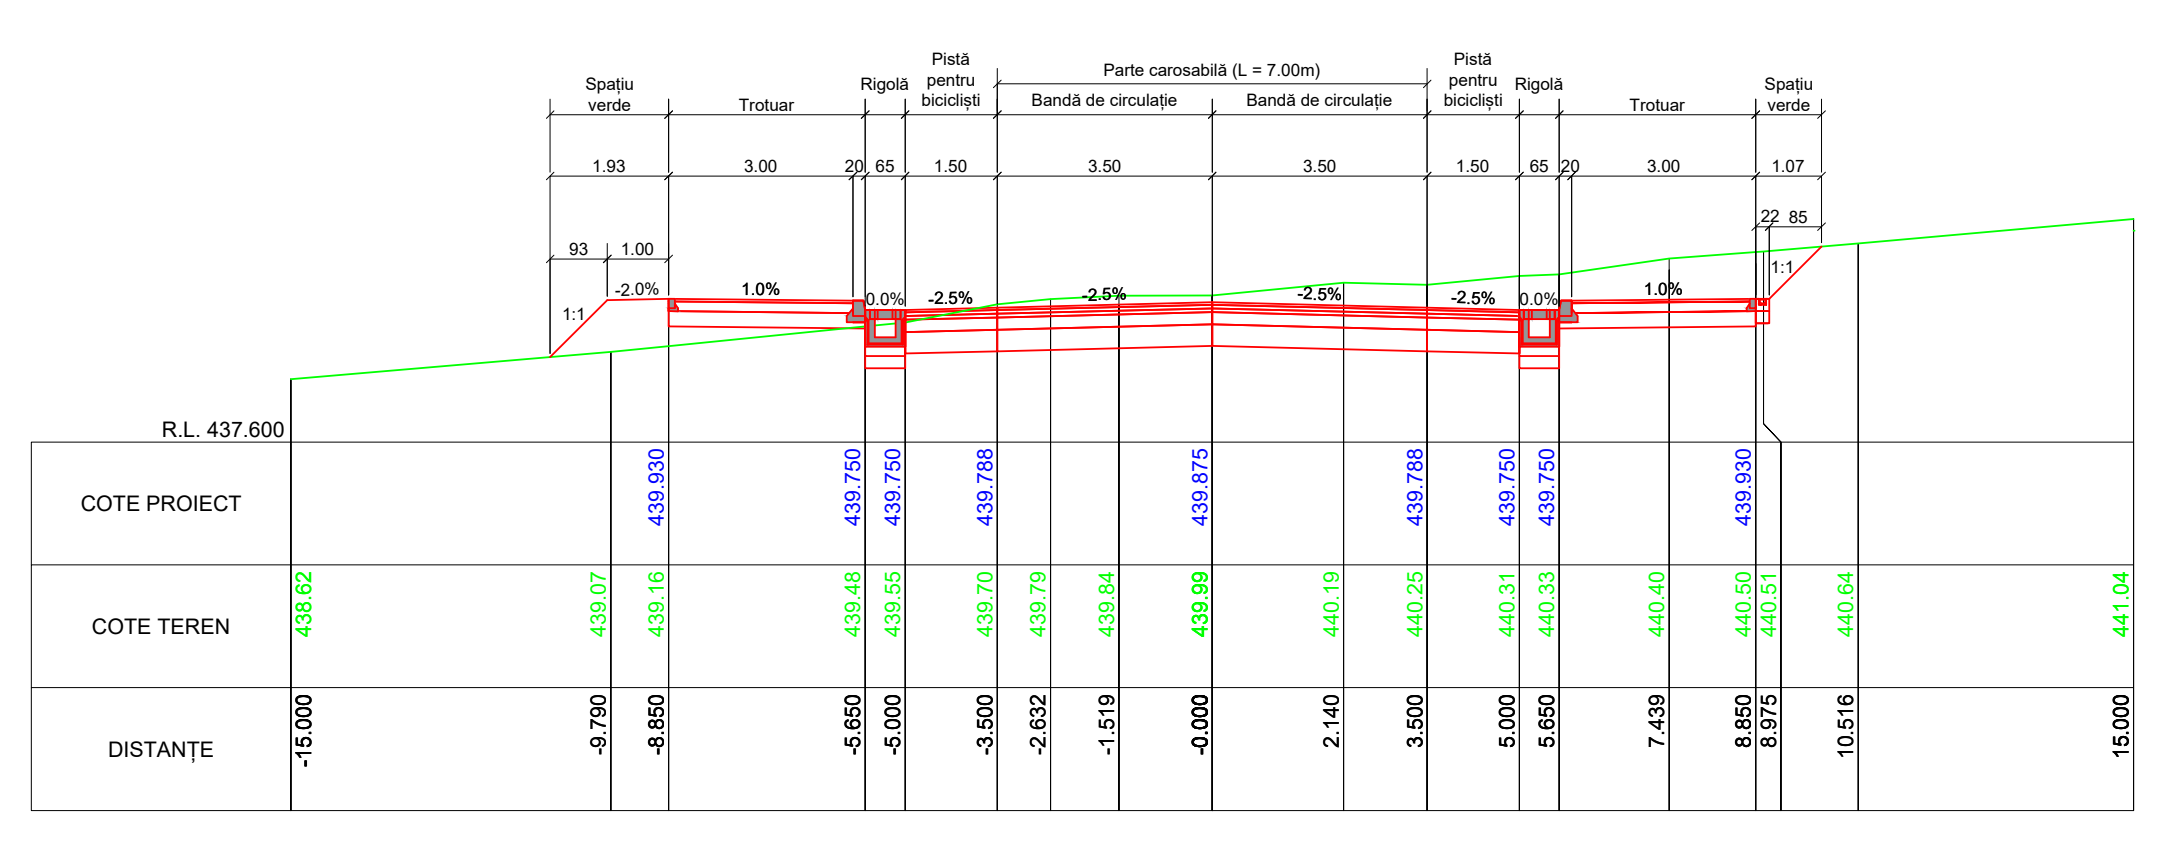
Km 530.000

PLAN DE SITUAȚIE

scara 1:500

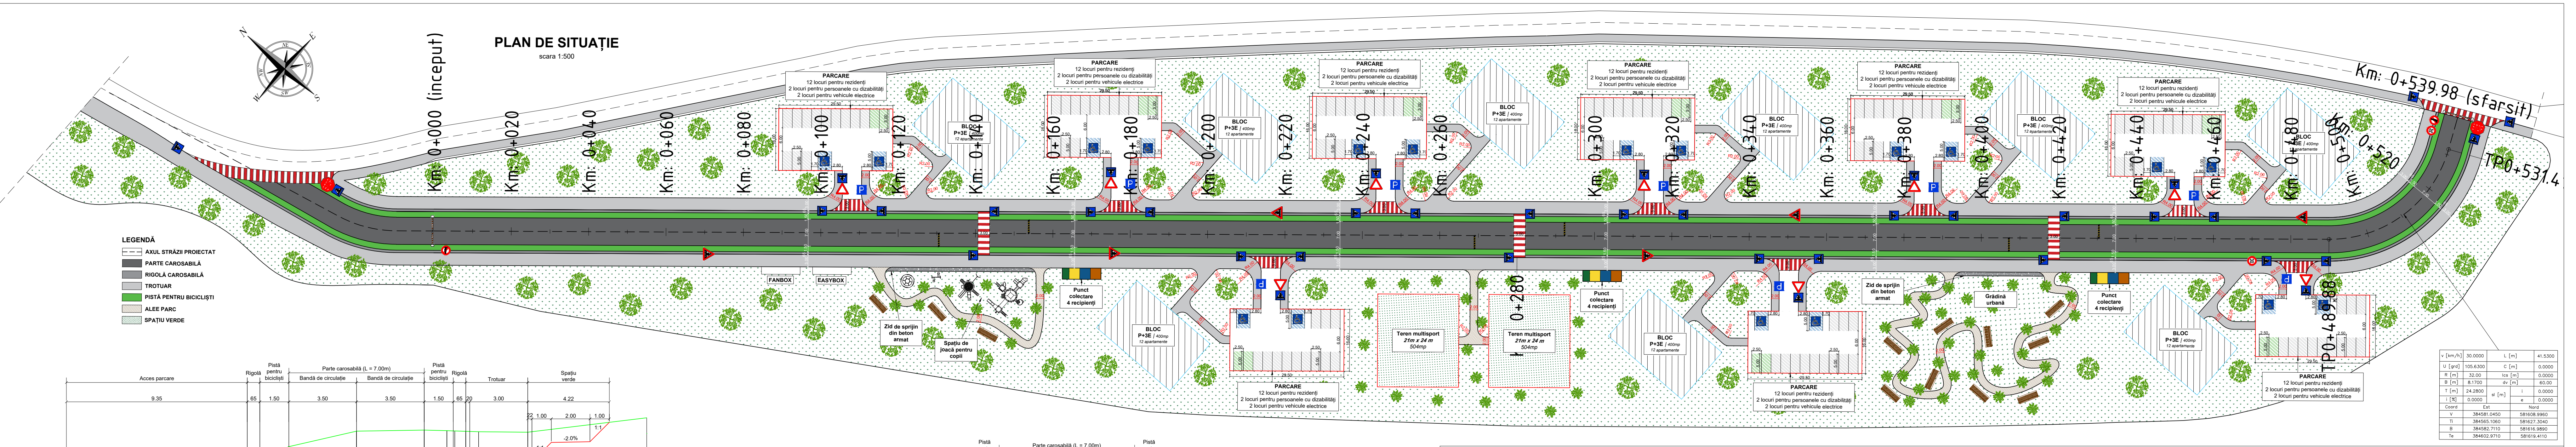

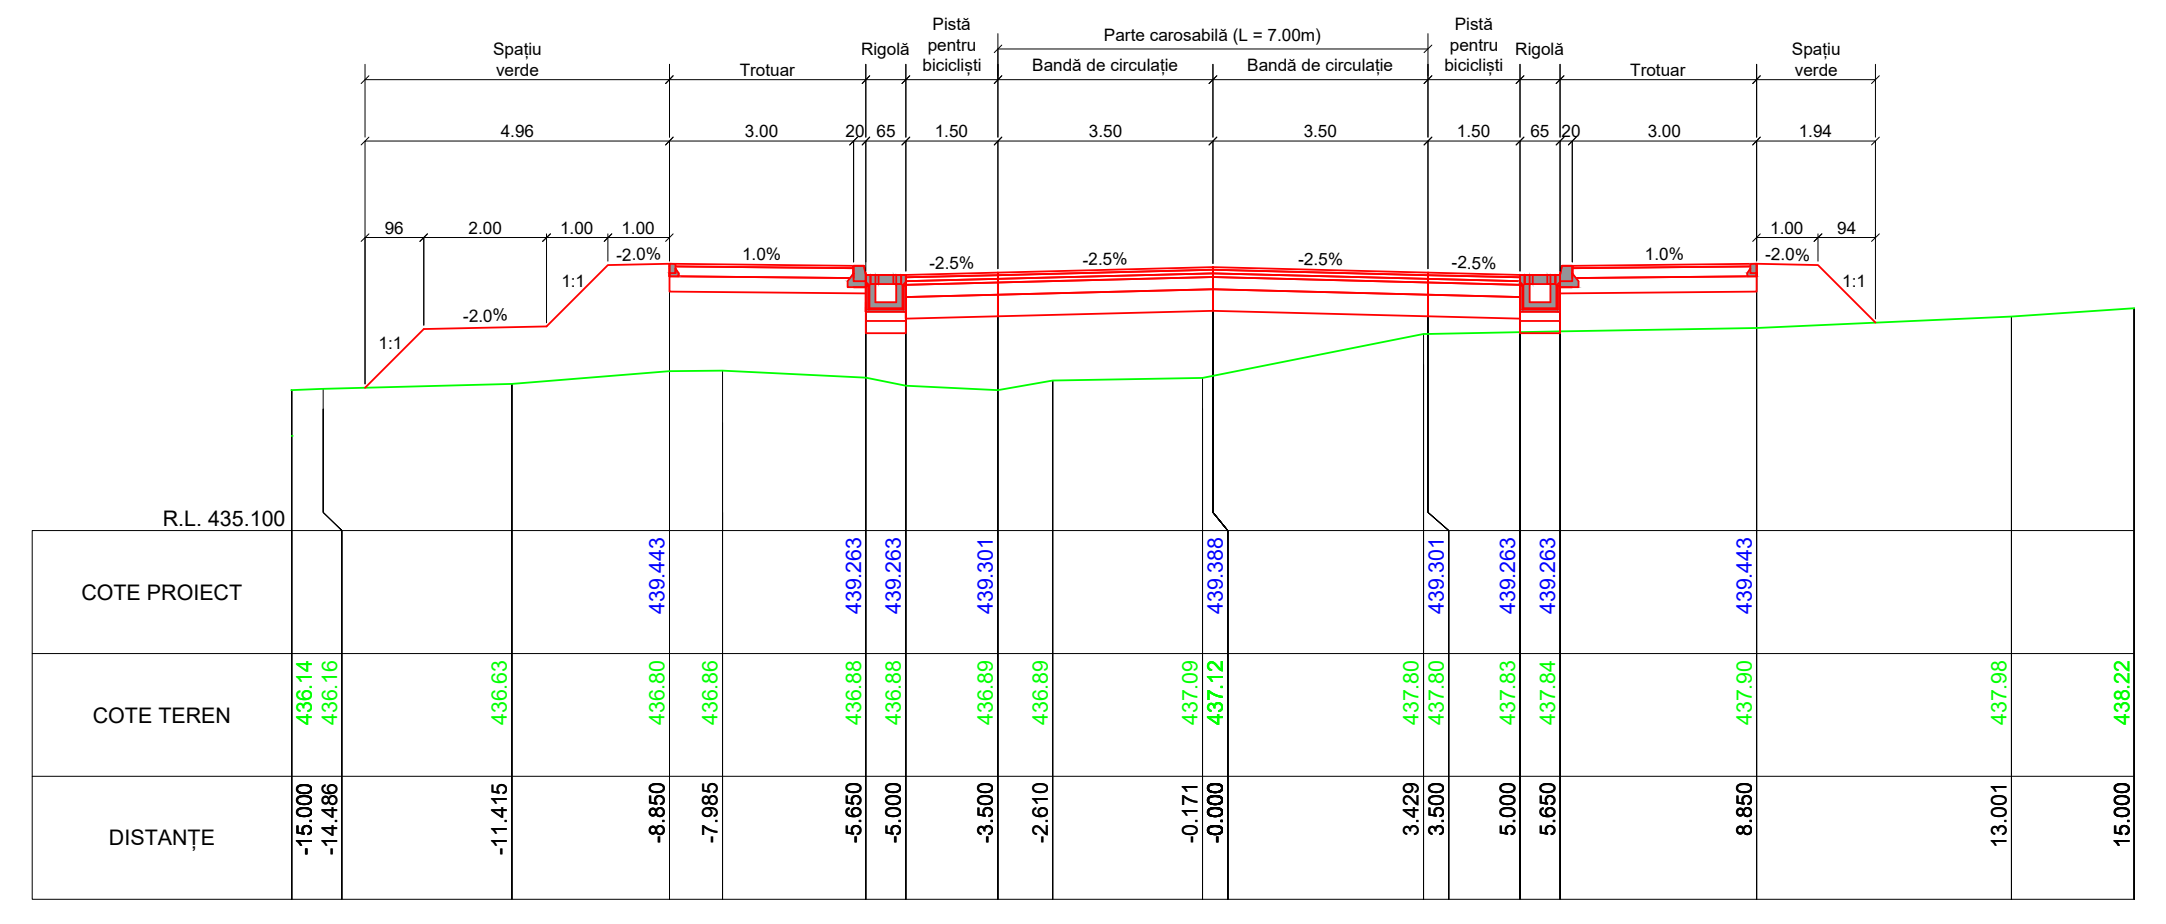
Km 539.978 (sfârșit traseu)

PROFIL LONGITUDINAL

scara 1:1000

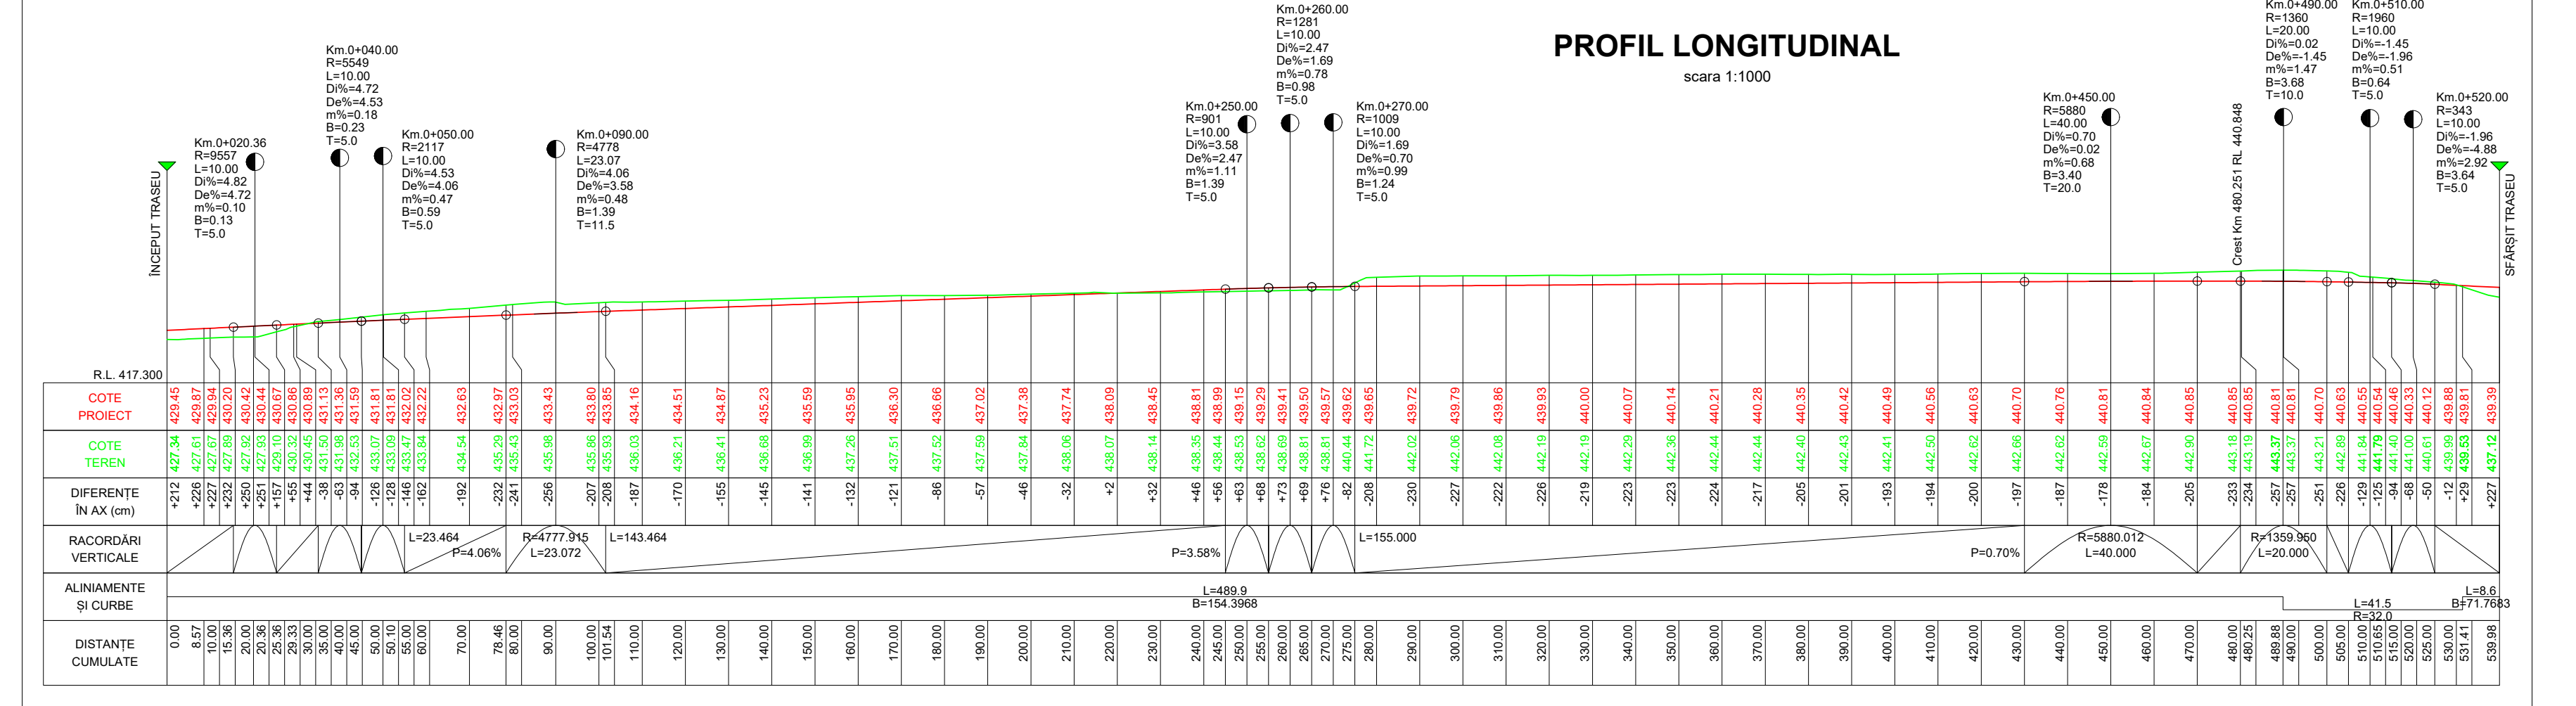

PLAN DE AMENAJARE PLATFORMĂ PARCARE

scara 1:100

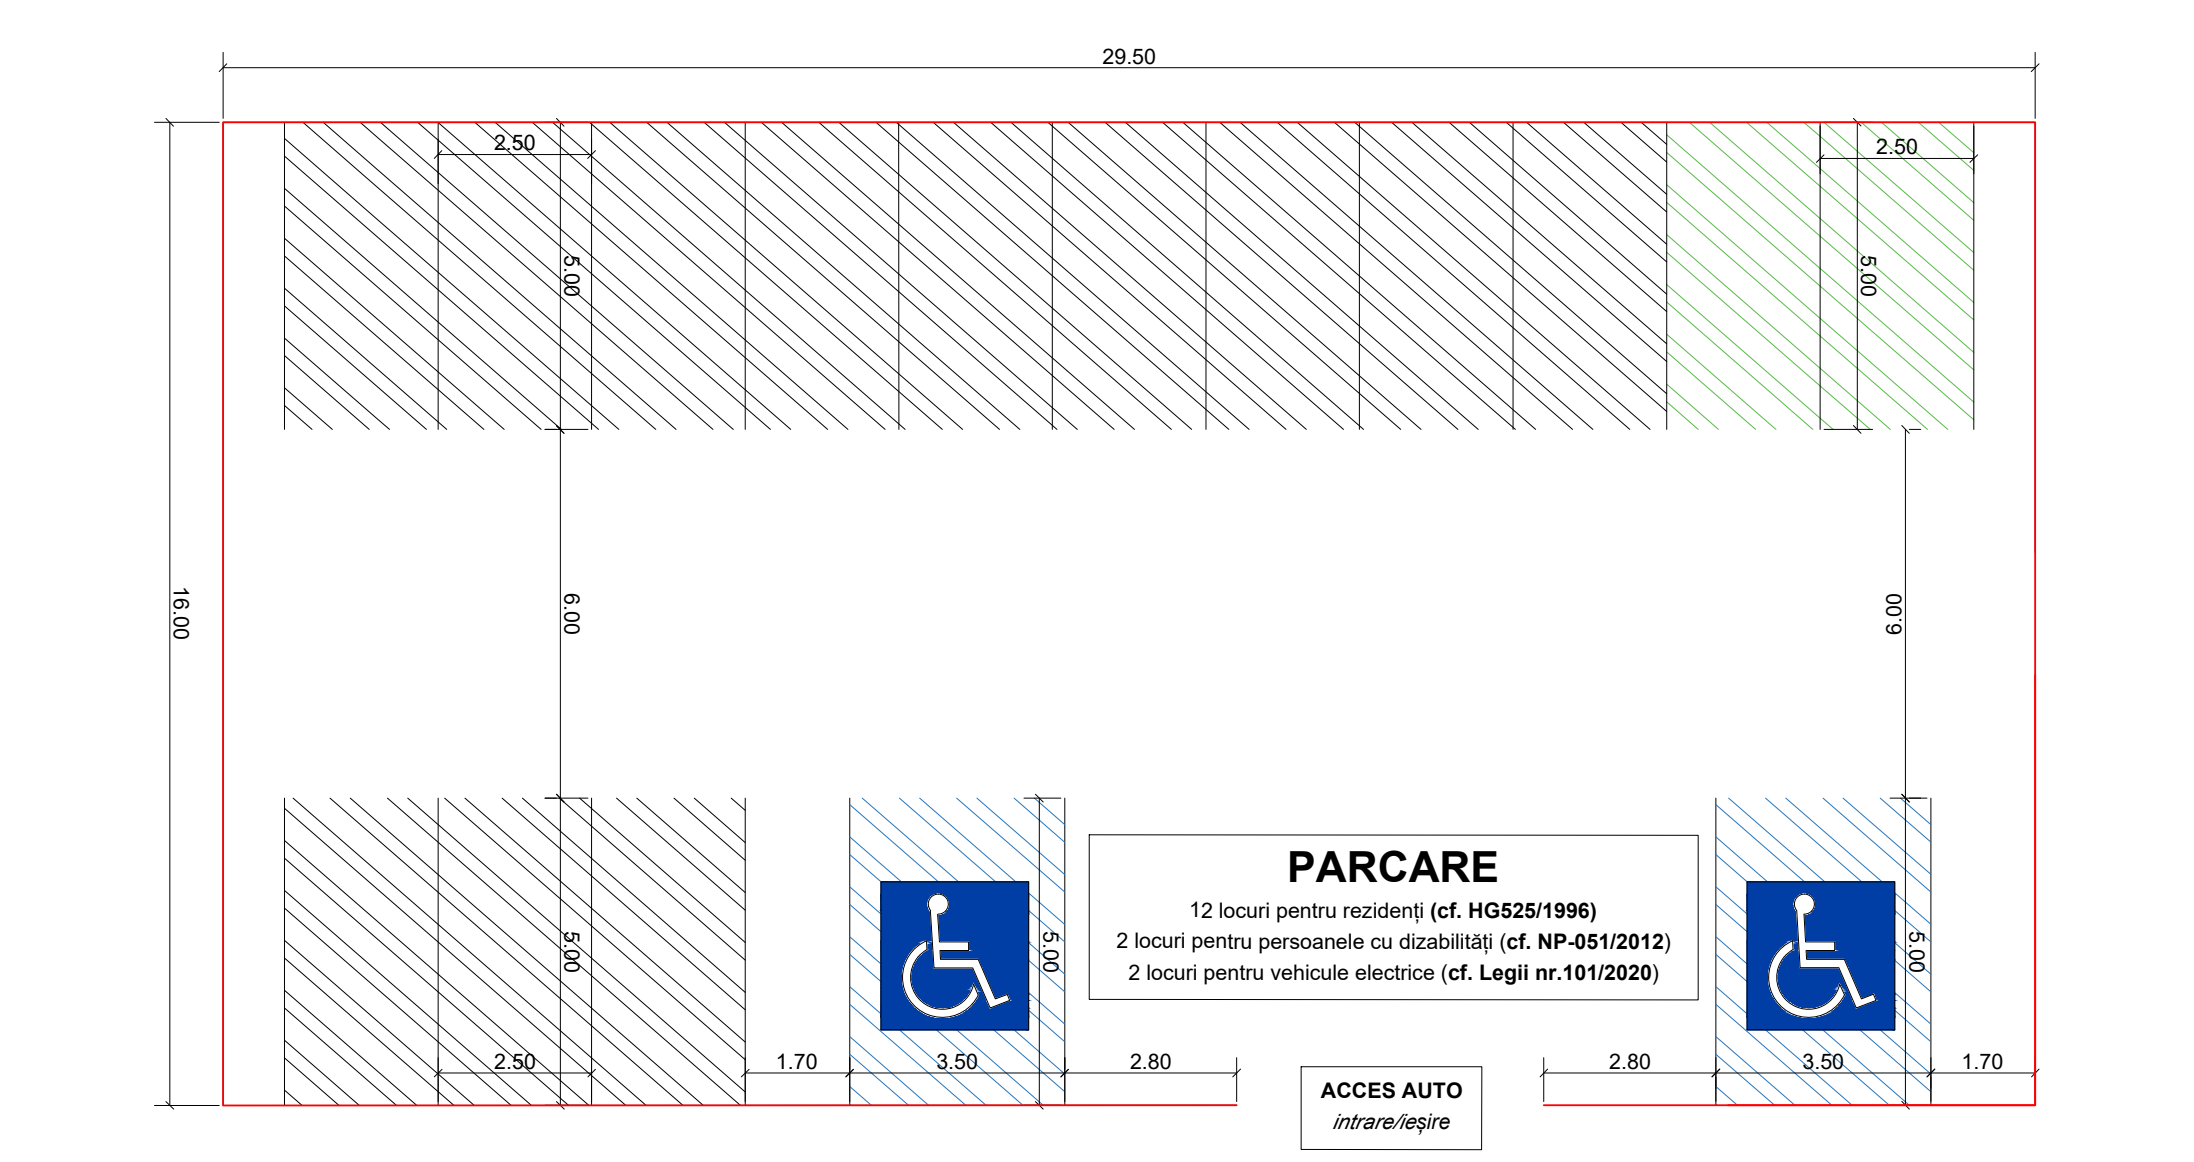

PARCARE

12 locuri pentru rezidenți **(cf. HG525/1996)**
2 locuri pentru persoanele cu dizabilități (**cf. NP-051/2012**)
2 locuri pentru vehicule electrice (**cf. Legii nr.101/2020**)

ACCES AUTO
intrare/ieșire

PROFIL TRANSVERSAL PLATFORMĂ PARCARE

scara 1:50

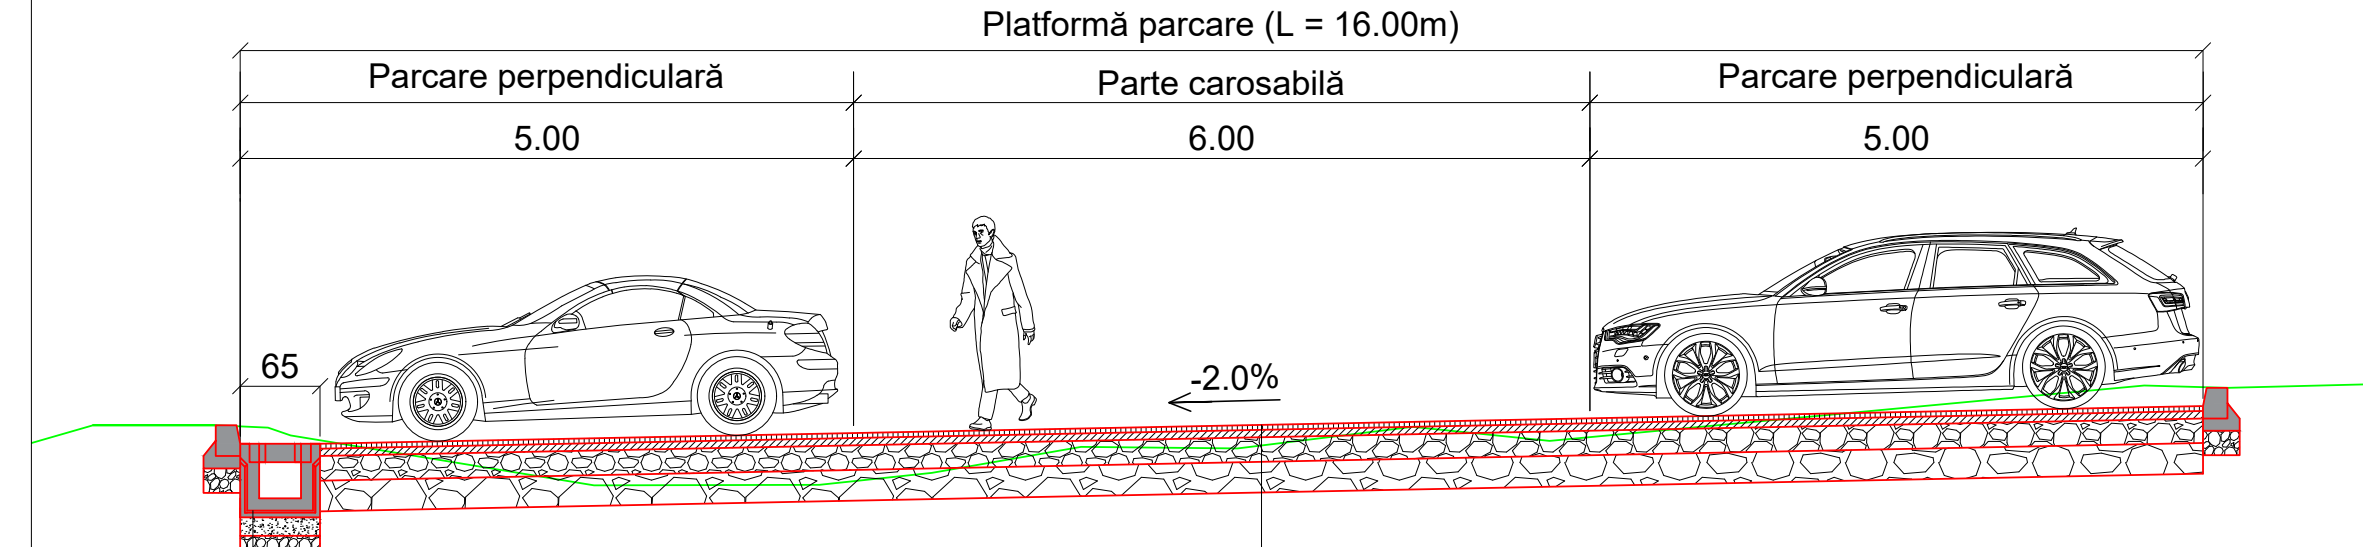

Rigolă prefabricată din beton C35/45
Beton C16/20 15cm
Balast 20cm

BA16 rul 50/70 4cm
BAD22.4 leg 50/70 6cm
Balast stabilizat cu ciment 20cm
Balast 35cm

DETALII DE EXECUȚIE

scara 1:20

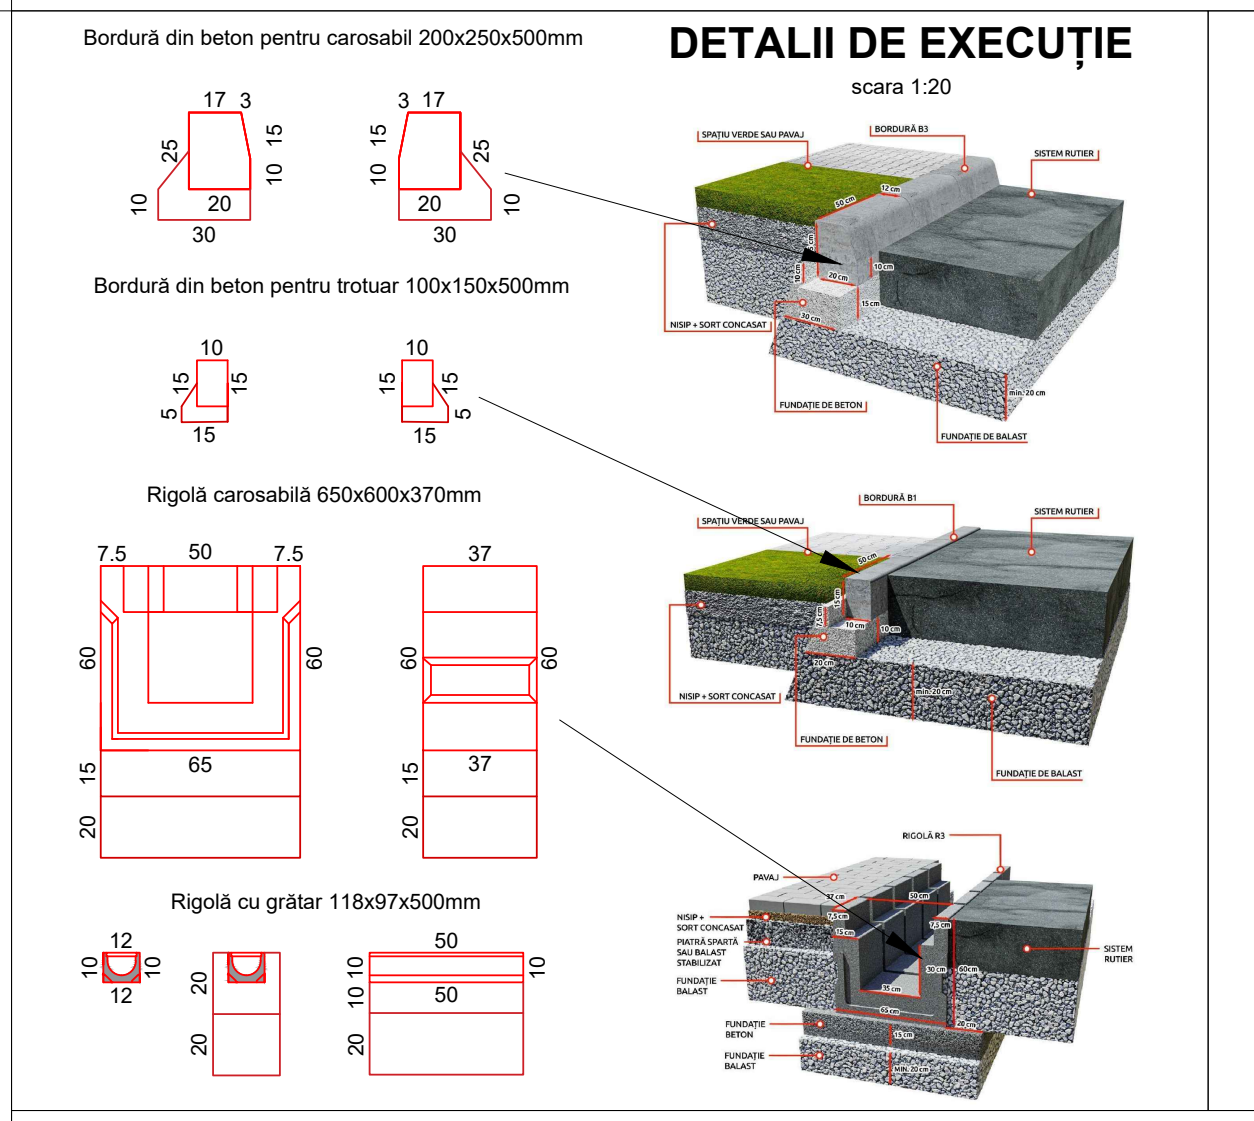
Bordură din beton pentru carosabil 200x250x500mm
Bordură din beton pentru trotuar 100x150x500mm
Rigolă carosabilă 650x600x370mm
Rigolă cu grătar 118x97x500mm
SPAȚIU VERDE SAU PAVAJ
BORDURĂ B3
BORDURĂ B1
RIGOLĂ R3
SISTEM RUTIER
NISIP + SORT CONCASAT
FUNDAȚIE DE BETON
FUNDAȚIE DE BALAST
PAVAJ
PIATRĂ SPARTĂ SAU BALAST STABILIZAT

SECȚIUNE TRANSVERSALĂ

ZID DE SPRIJIN DIN BETON ARMAT
scara 1:50

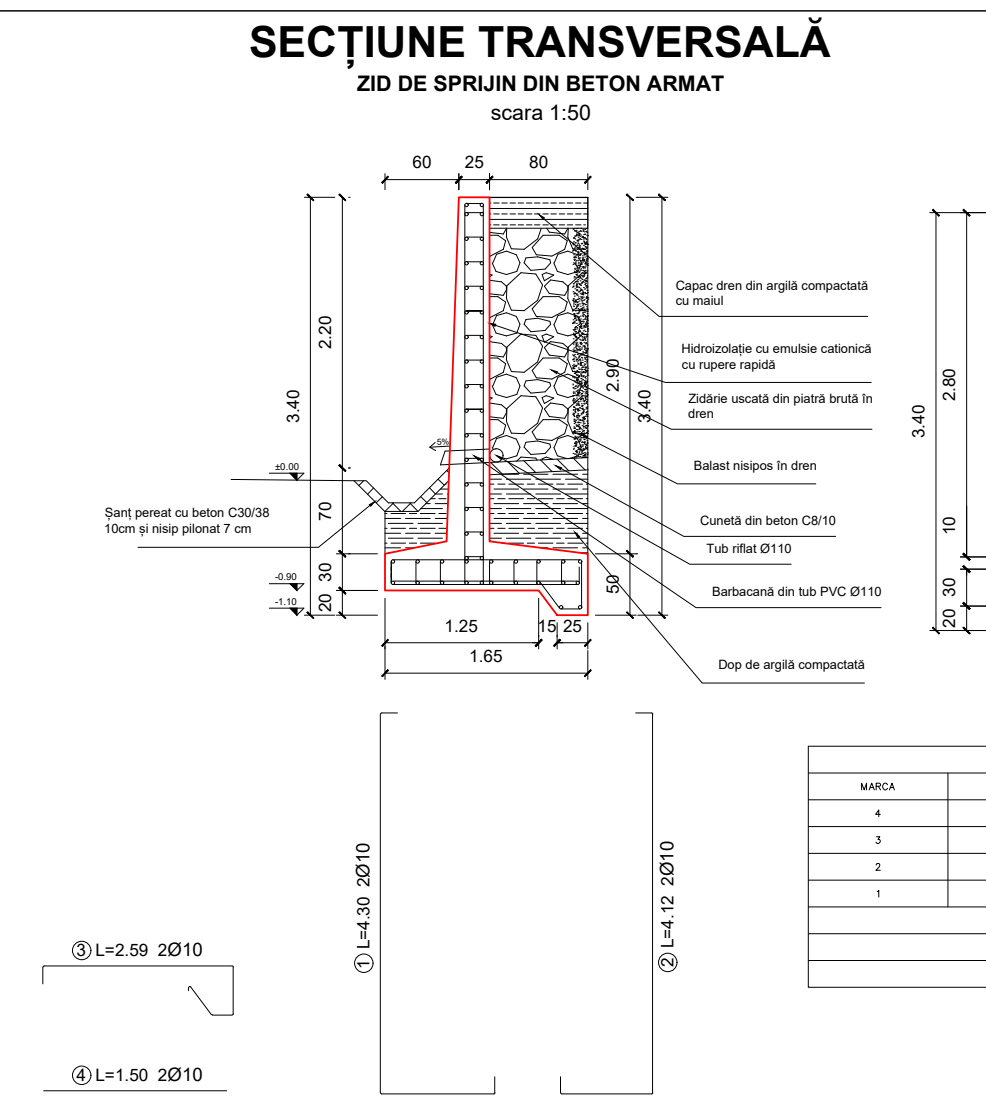
Capac dren din argilă compactată cu maiul
Hidroizolație cu emulsie cationică cu rupere rapidă
Zidărie uscată din piatră brută în dren
Balast nisipos în dren
Cunetă din beton C8/10
Tub riflat Ø110
Barbacană din tub PVC Ø110
Dop de argilă compactată
Șanț pereat cu beton C30/38 10cm și nisip pilonat 7 cm
① L=4.30 2Ø10
② L=4.12 2Ø10
③ L=2.59 2Ø10
④ L=1.50 2Ø10

ELEVAȚIE

ZID DE SPRIJIN DIN BETON ARMAT
scara 1:50

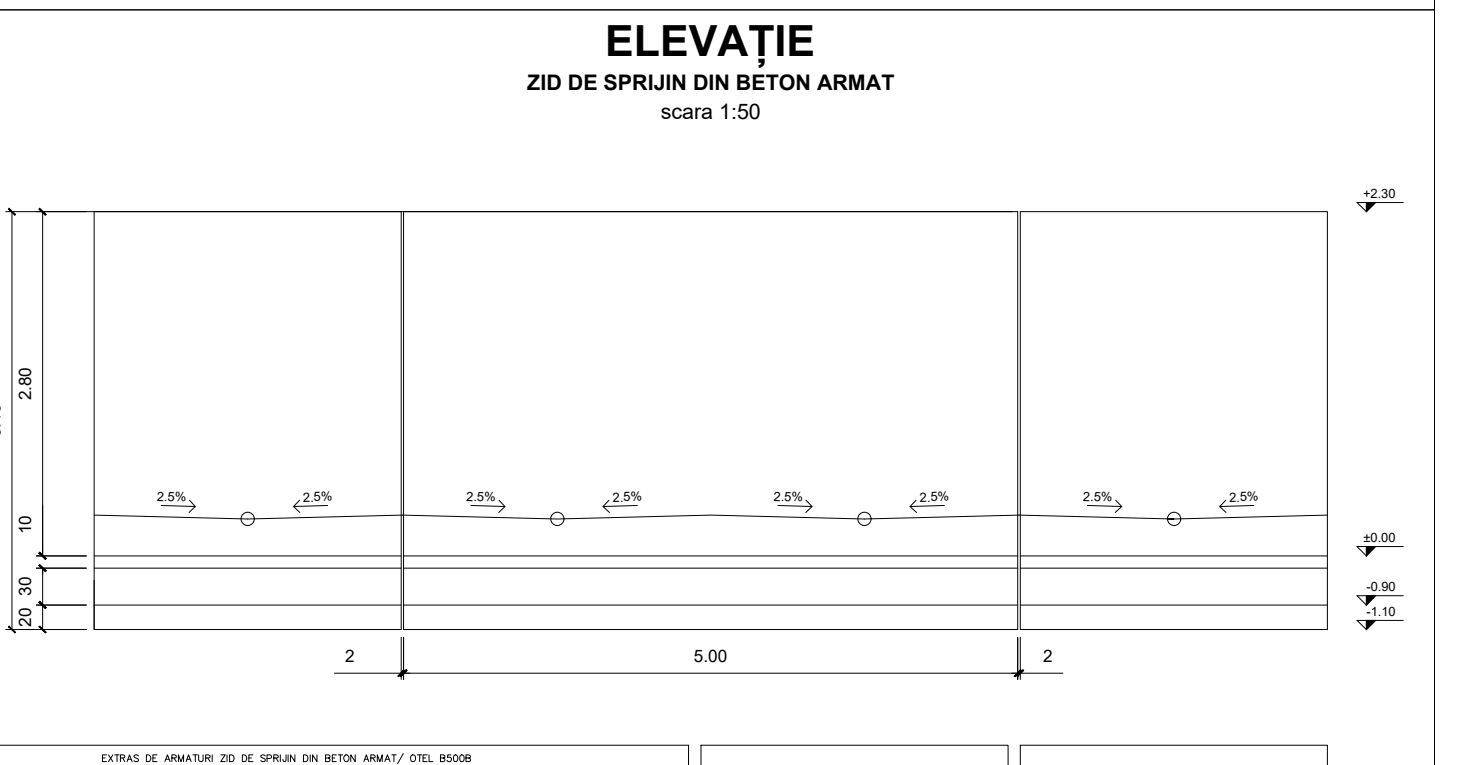

EXTRAS DE ARMATURI ZID DE SPRIJIN DIN BETON ARMAT/ OTEL B500B

MARCA	DIAMETRU	LUNGIME	MASA [kg/ml]	NR. BUC.	LUNGIMI PE DIAMETRE [ml]	GREUTATE [kg]
4	10.0000	1.50	0.6170	2102	3153.00	1945.40
3	10.0000	2.59	0.6170	2102	5444.18	3359.06
2	10.0000	4.12	0.6170	2102	8660.24	5343.37
1	10.0000	4.30	0.6170	2102	9038.60	5576.82
TOTAL LUNGIMI PE DIAMETRE [ml]						26296.02
GREUTATE PE DIAMETRE [kg]						16225.00
GREUTATE TOTALA [kg]						16225.00

ELEVAȚIE ZID DE SPRIJIN

Beton: C35/45
Oțel: B500B
Clasă de expunere: XD3
Valoare maximă A/C: 0.60
Dozaj minim ciment (kg/m³): 300

FUNDAȚIE ZID SPRIJIN

Beton: C35/45
Oțel: B500B
Clasă de expunere: XF3
Valoare maximă A/C: 0.65
Dozaj minim ciment (kg/m³): 300

PROFIL TRANSVERSAL TIP

scara 1:50

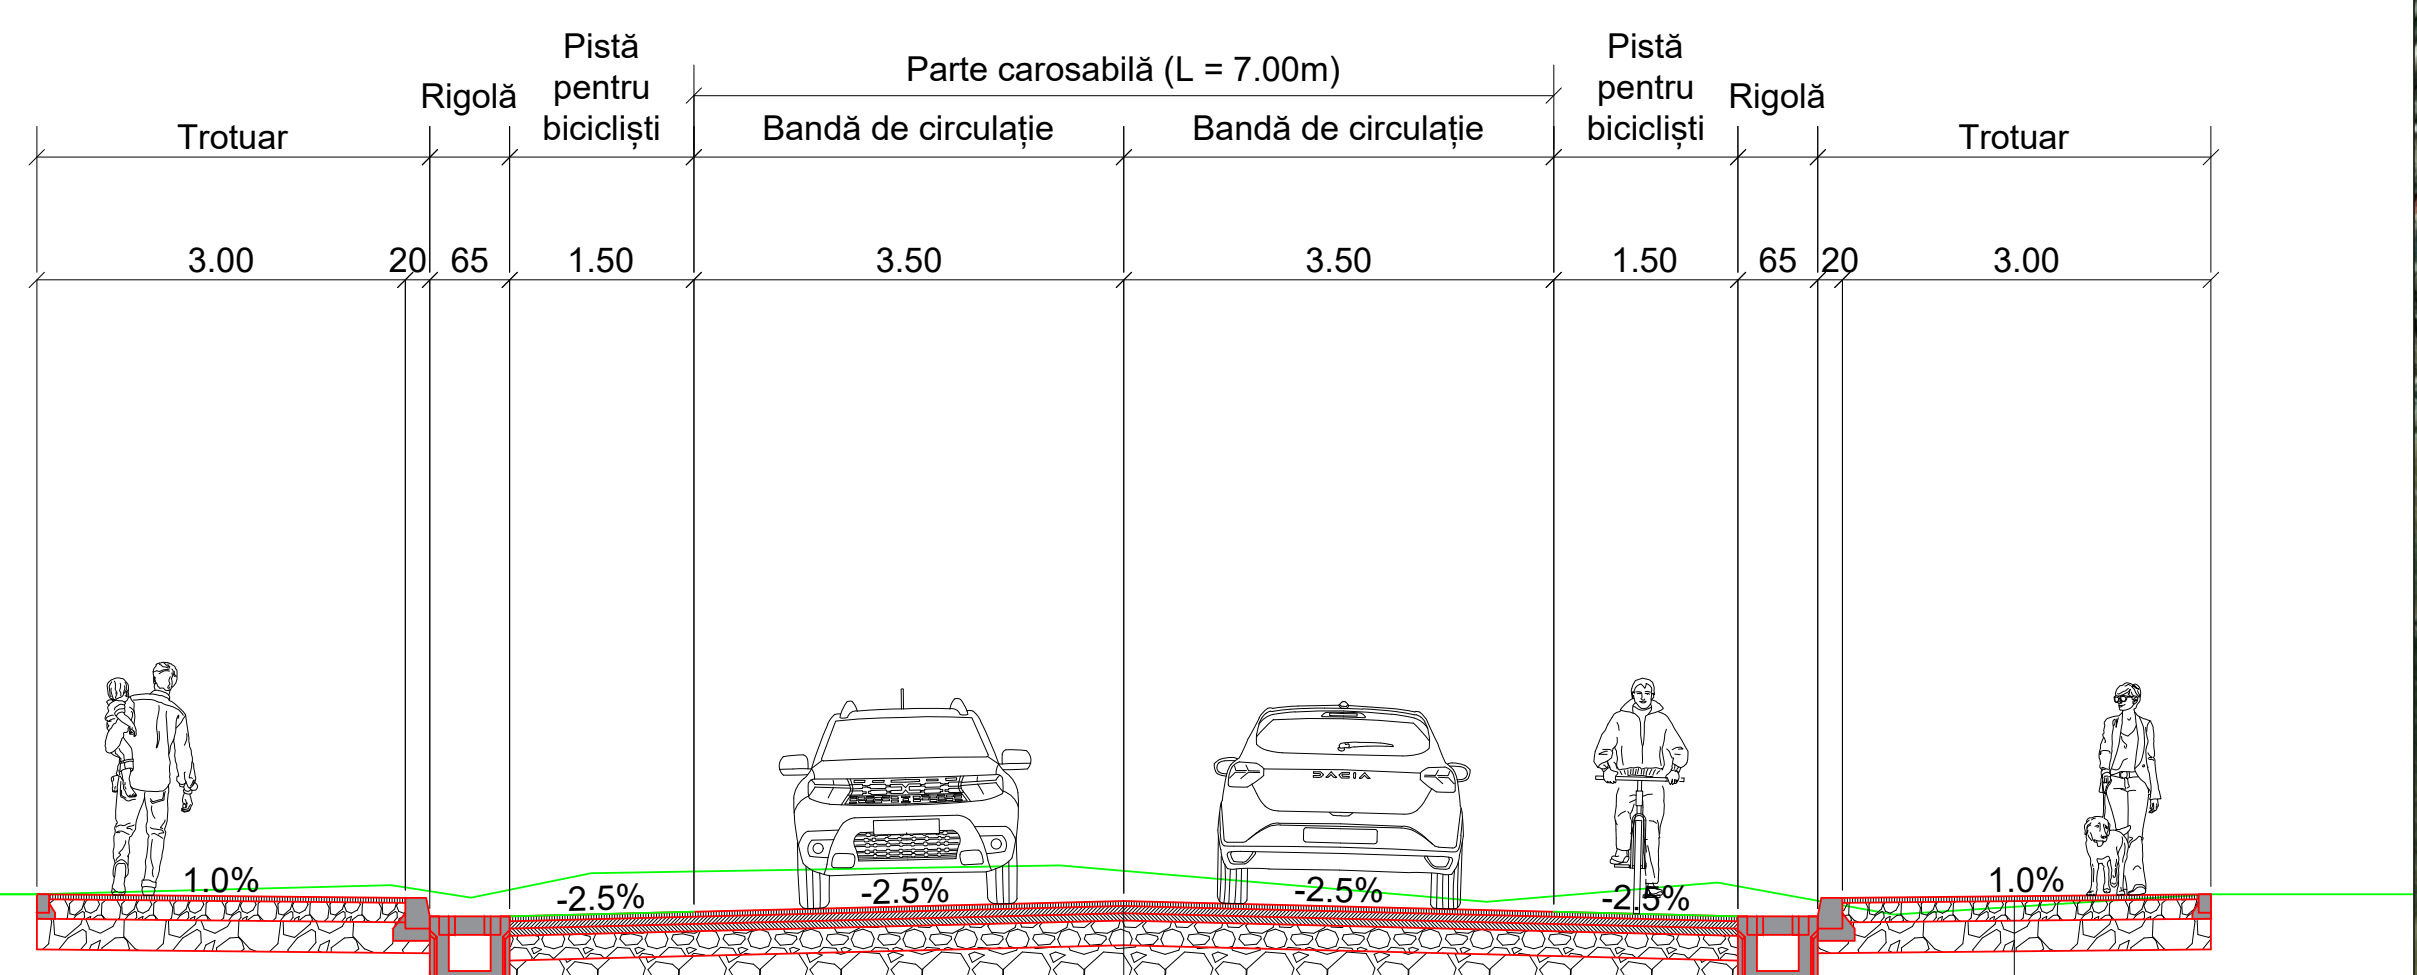

Rigolă prefabricată din beton C35/45
Beton C16/20 15cm
Balast 20cm

BA16 rul 50/70 4cm
BAD22.4 leg 50/70 6cm
AB22.4 baza 50/70 6cm
Balast stabilizat cu ciment 20cm
Balast 35cm

BA8 rul 50/70 4cm
Balast stabilizat 16cm
Balast 25cm

UNIVERSITATEA TEHNICĂ CLUJ-NAPOCA FACULTATEA DE CONSTRUCȚII			PROIECT DE DIPLOMĂ *Analiza și proiectarea infrastructurii rutiere pentru un ansamblu rezidențial în context urban*		PROIECT 01/2025
	NUME	SEMNĂTURĂ	SCARA 1:1000 1:500 1:100 1:50 1:20	Plan de situație Profil longitudinal Profile transversale Profil transversal tip stradă + parcare Plan amenajare parcare Secțiune transversală și elevație zid de sprijin Detalii de execuție	PLANȘA 1
DESENAT	Harapciuc Bernard Alexandru		DATA 16.06.2025		
VERIFICAT	Șef. L. Dr. Ing. Clitan Andrei Florin				